
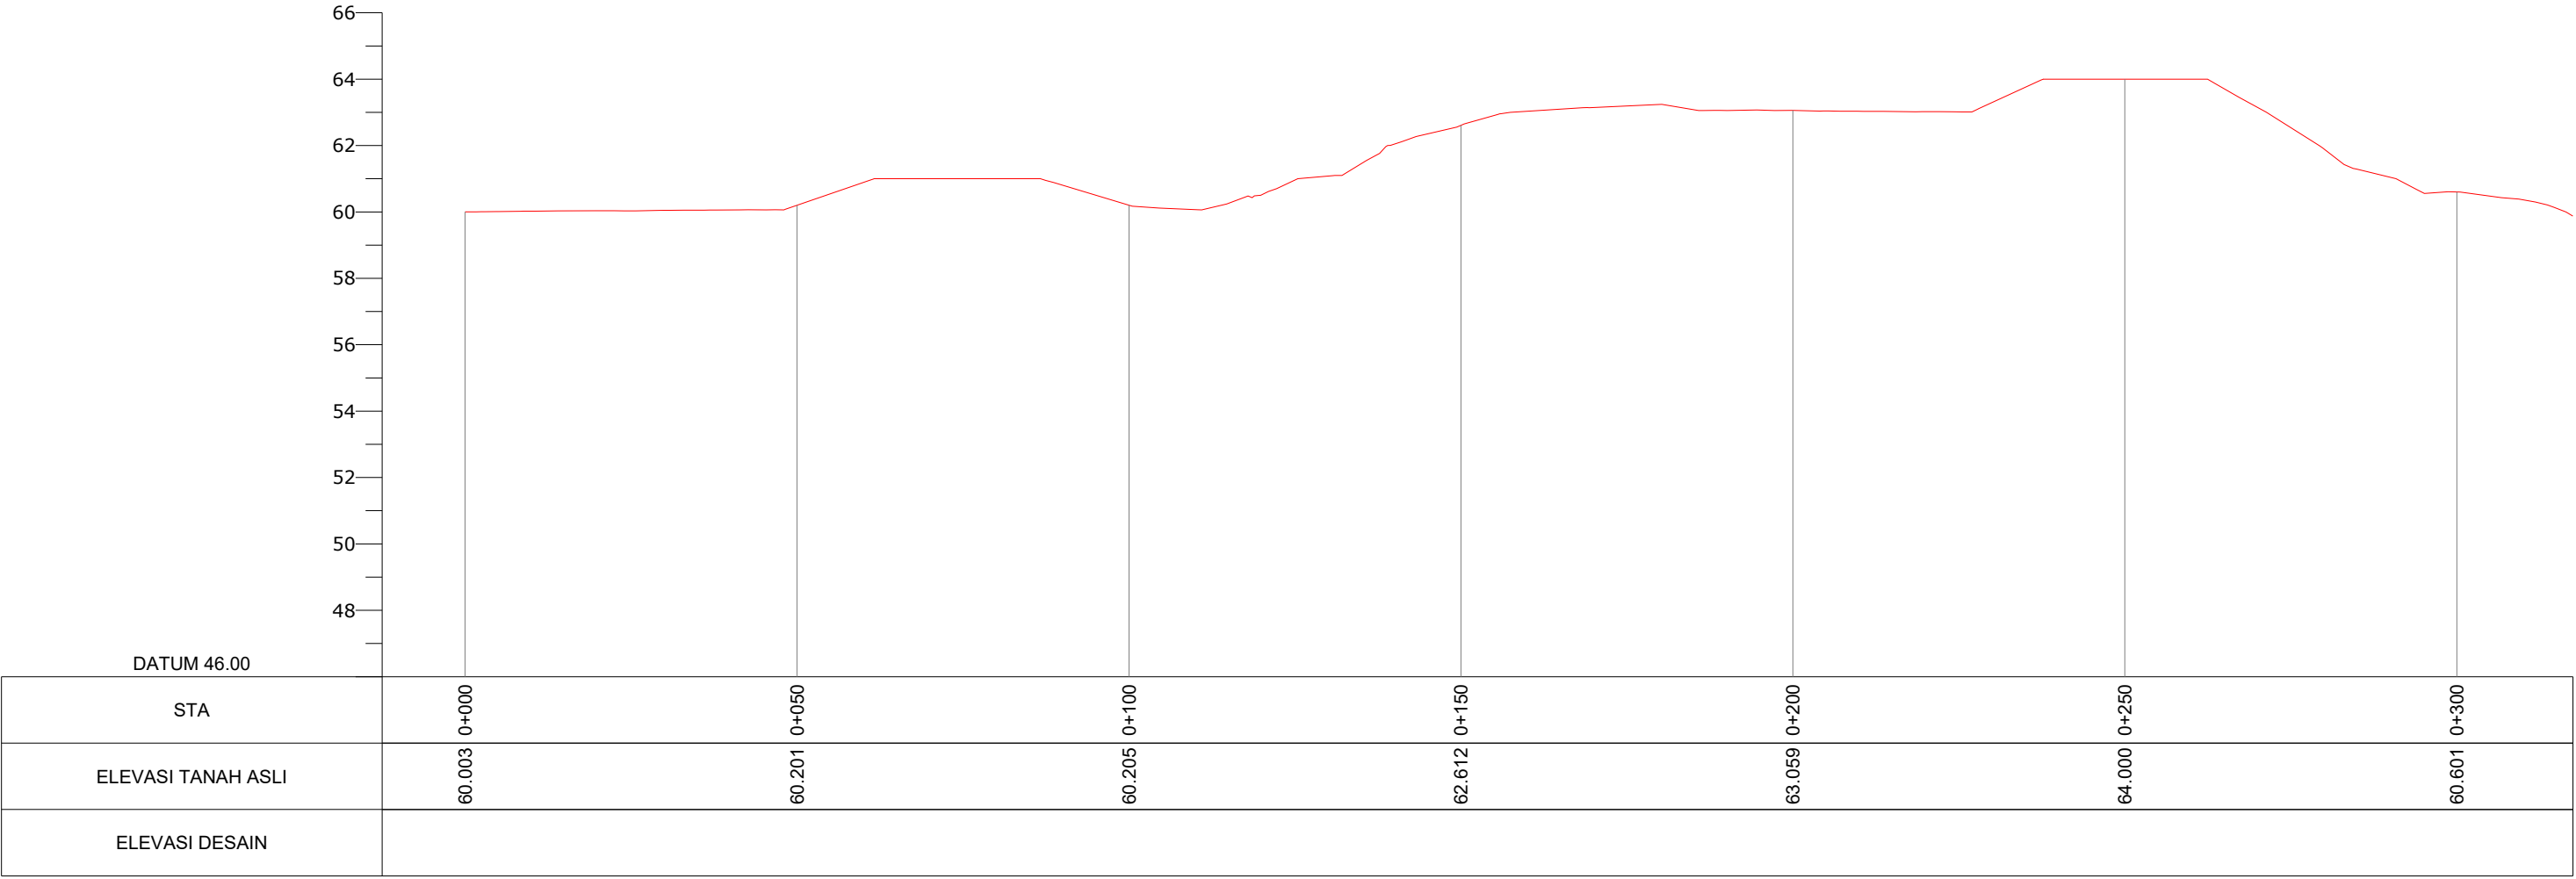
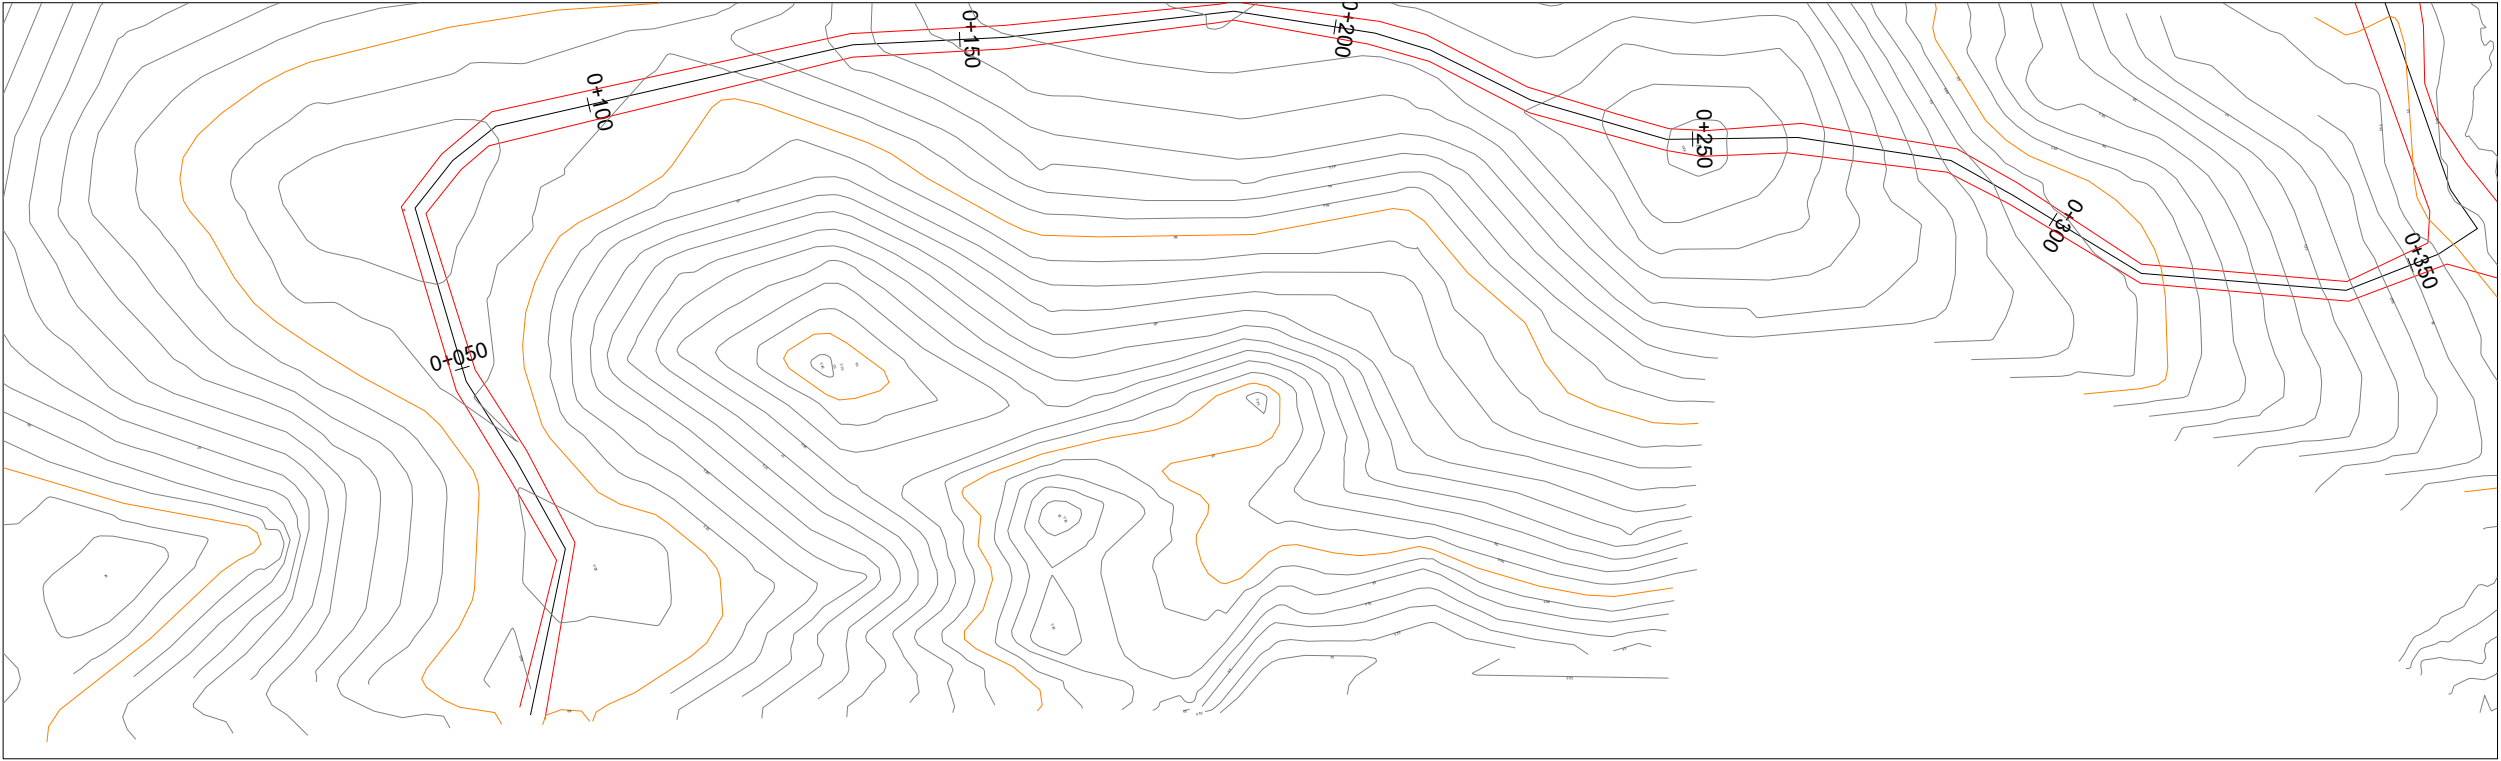


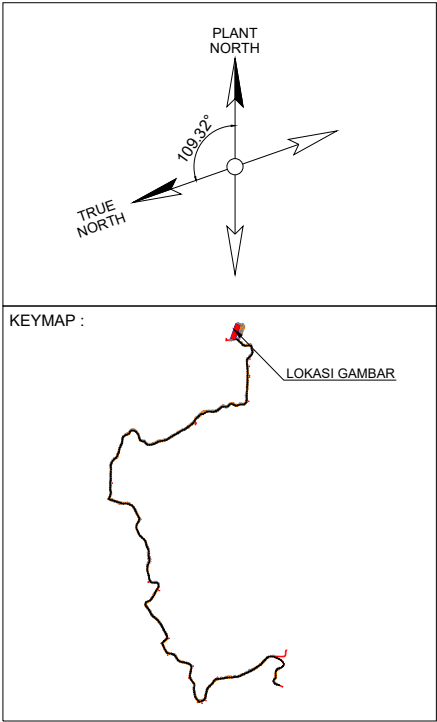

NOTES

1. ALL DIMENSIONS ARE MEASURED IN METER

LEGEND

BUILDING

ROAD

BRIDGE

RIVER

DRAINAGE

FENCE

CONTROL POINT (CP)

BENCH MARK (BM)

MAJOR CONTOUR

MINOR CONTOUR

REFERENCE DWG NO.

TITLE

REV. NO.

DATE

DESCRIPTION

DRWN

CHK'D

APP'D

APP'D

OWNER:

skkmigas

PERTAMINA EP

CONSULTANT:

SUCOFINDO

PROJECT TITLE :

Survey Pemetaan, Desain Siteplan Lokasi Bor CLA-001

DOC. NO. :

CONTRACT NO. : 4710001475

TITLE :

PETA SITUASI DAN LONG SECTION

SCALE

1 : 1,000

1 : 200

DRAWING NO.



-

REV.

0

SIZE

A3

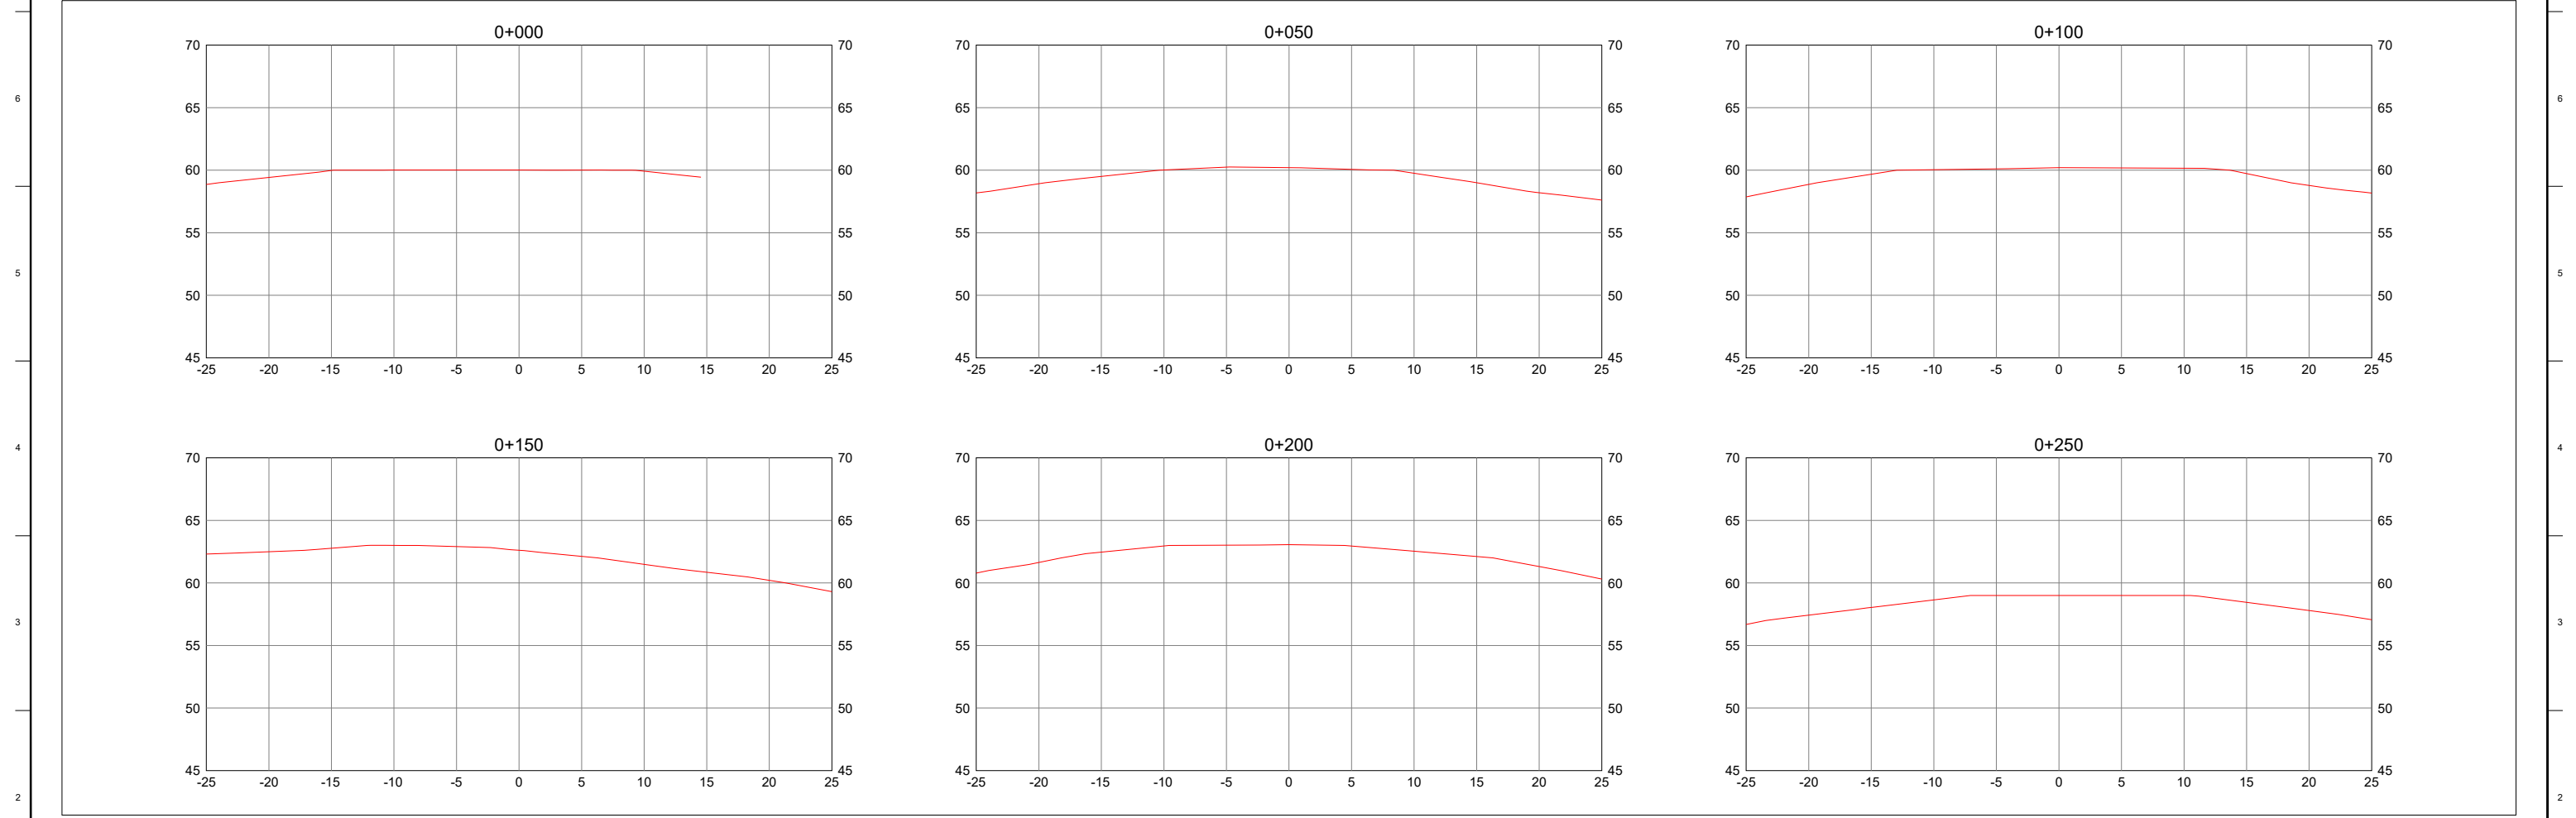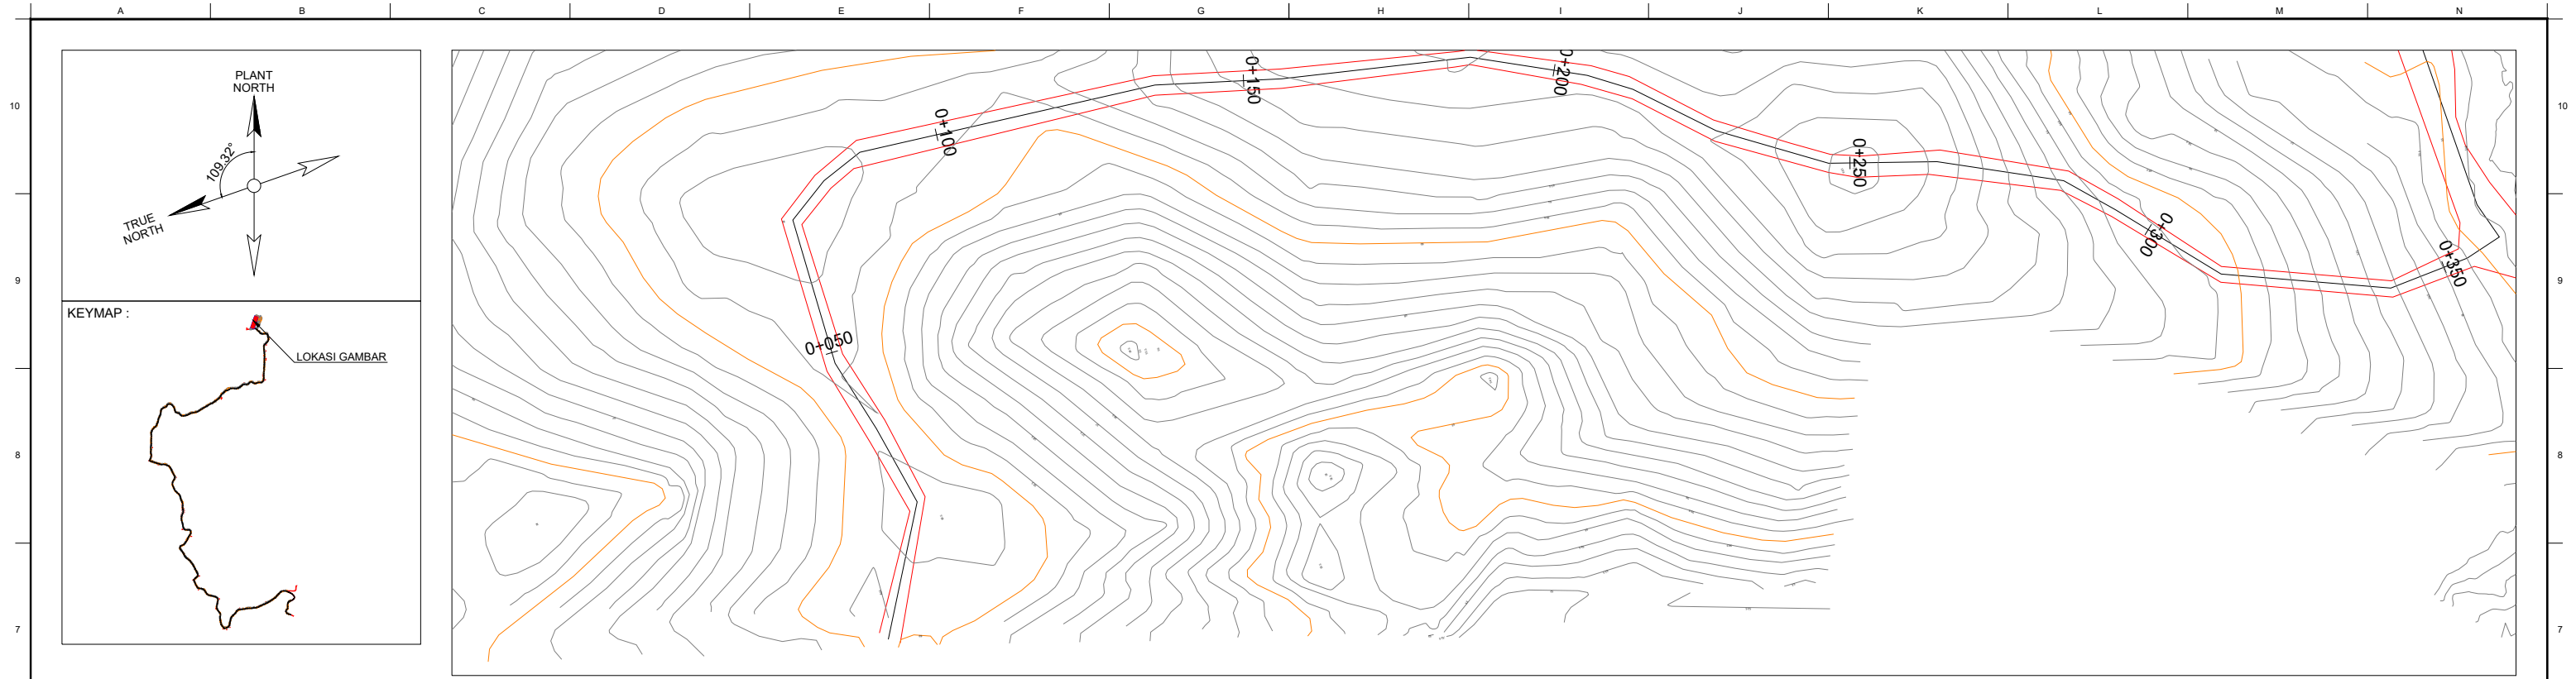

NOTES

1. ALL DIMENSIONS ARE MEASURED IN METER

LEGEND

:BUILDING

:ROAD

:BRIDGE

:RIVER

:DRAINAGE

:FENCE

:CONTROL POINT (CP)

:BENCH MARK (BM)

:MAJOR CONTOUR

:MINOR CONTOUR

REFERENCE DWG NO.

TITLE

REV. NO.

DATE

DESCRIPTION

DRWN

CHK'D

APP'D

APP'D

skkmigas

PERTAMINA EP

SUCOFINDO

OWNER:

PROJECT TITLE :
Survey Pemetaan, Desain Siteplan Lokasi Bor CLA-001

DOC. NO. :
CONTRACT NO. : 4710001475

TITLE :
PETA SITUASI DAN CROSS SECTION

SCALE

DRAWING NO.

REV.

SIZE

1 : 1.000

-

0

A3