

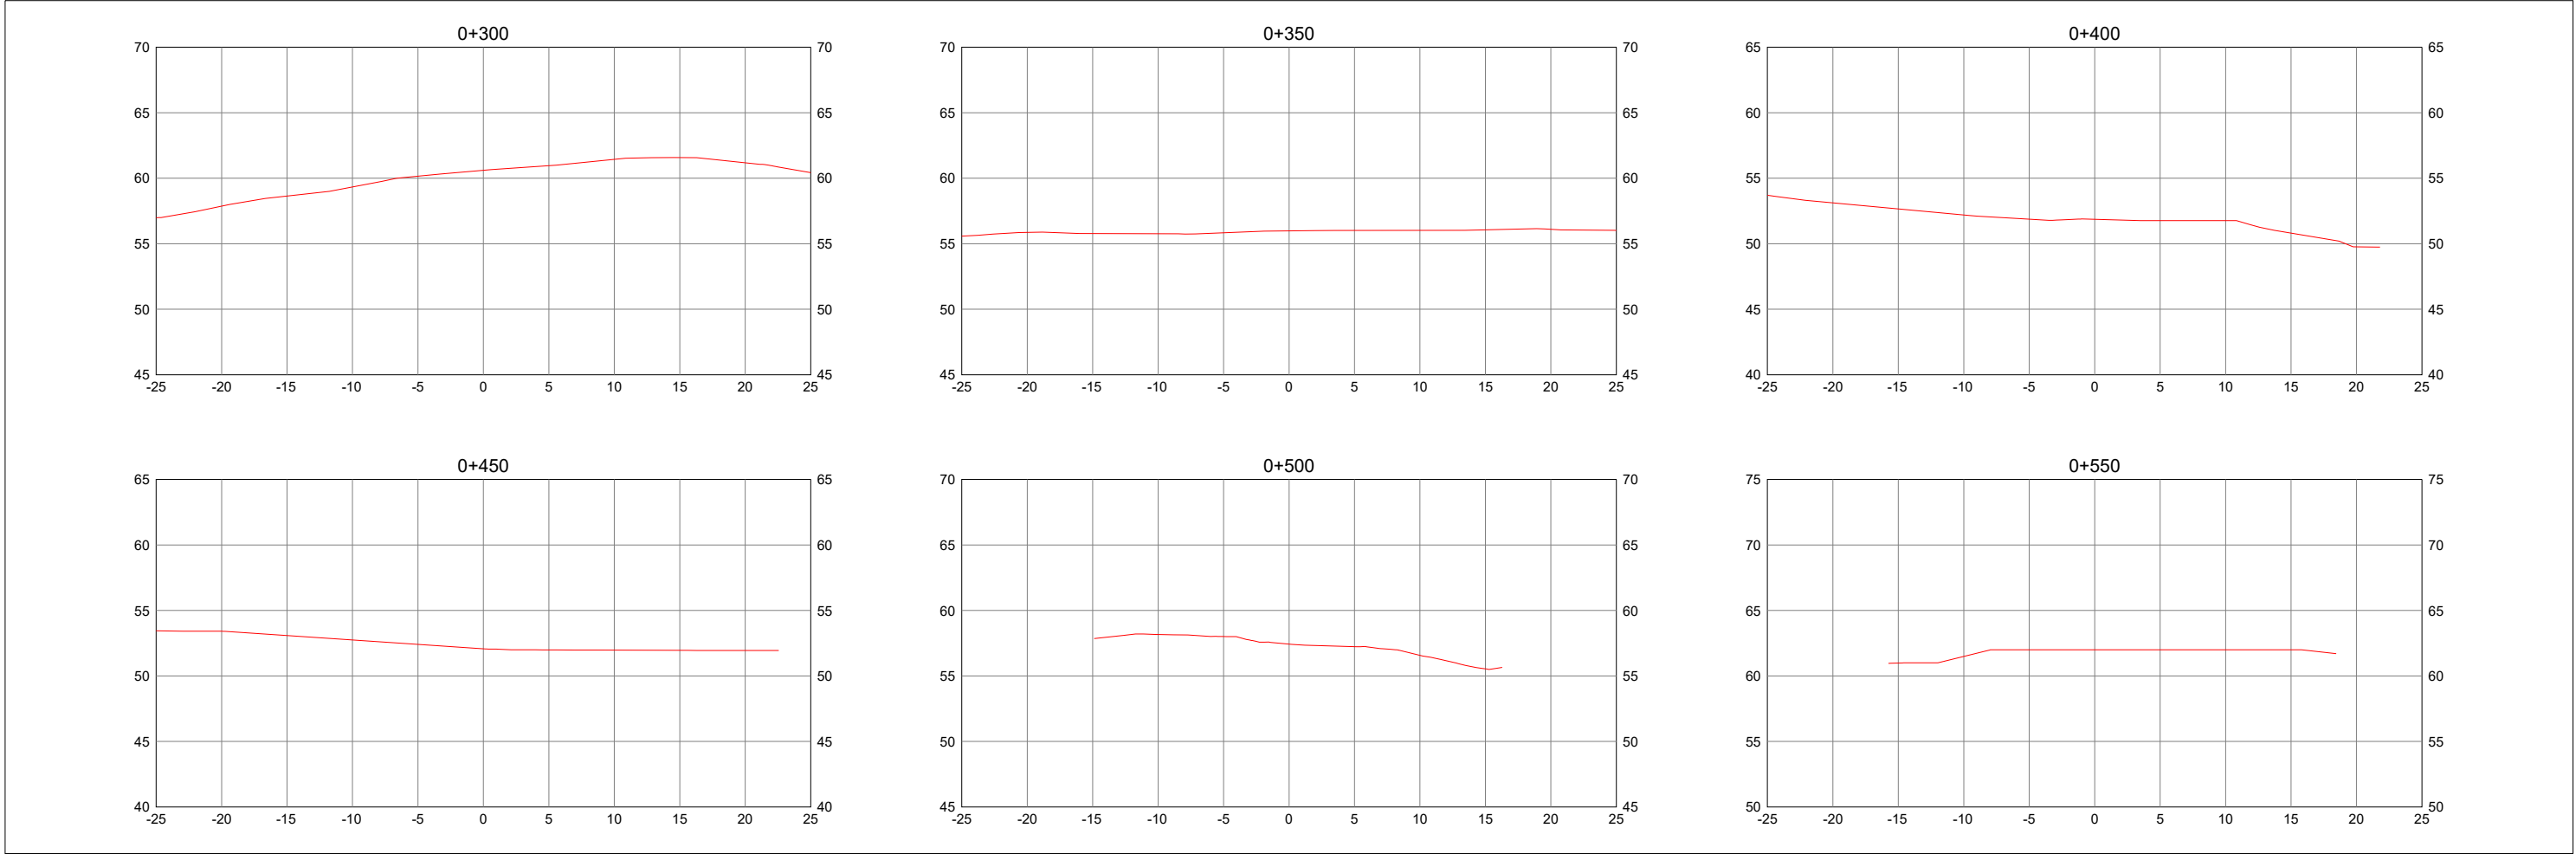
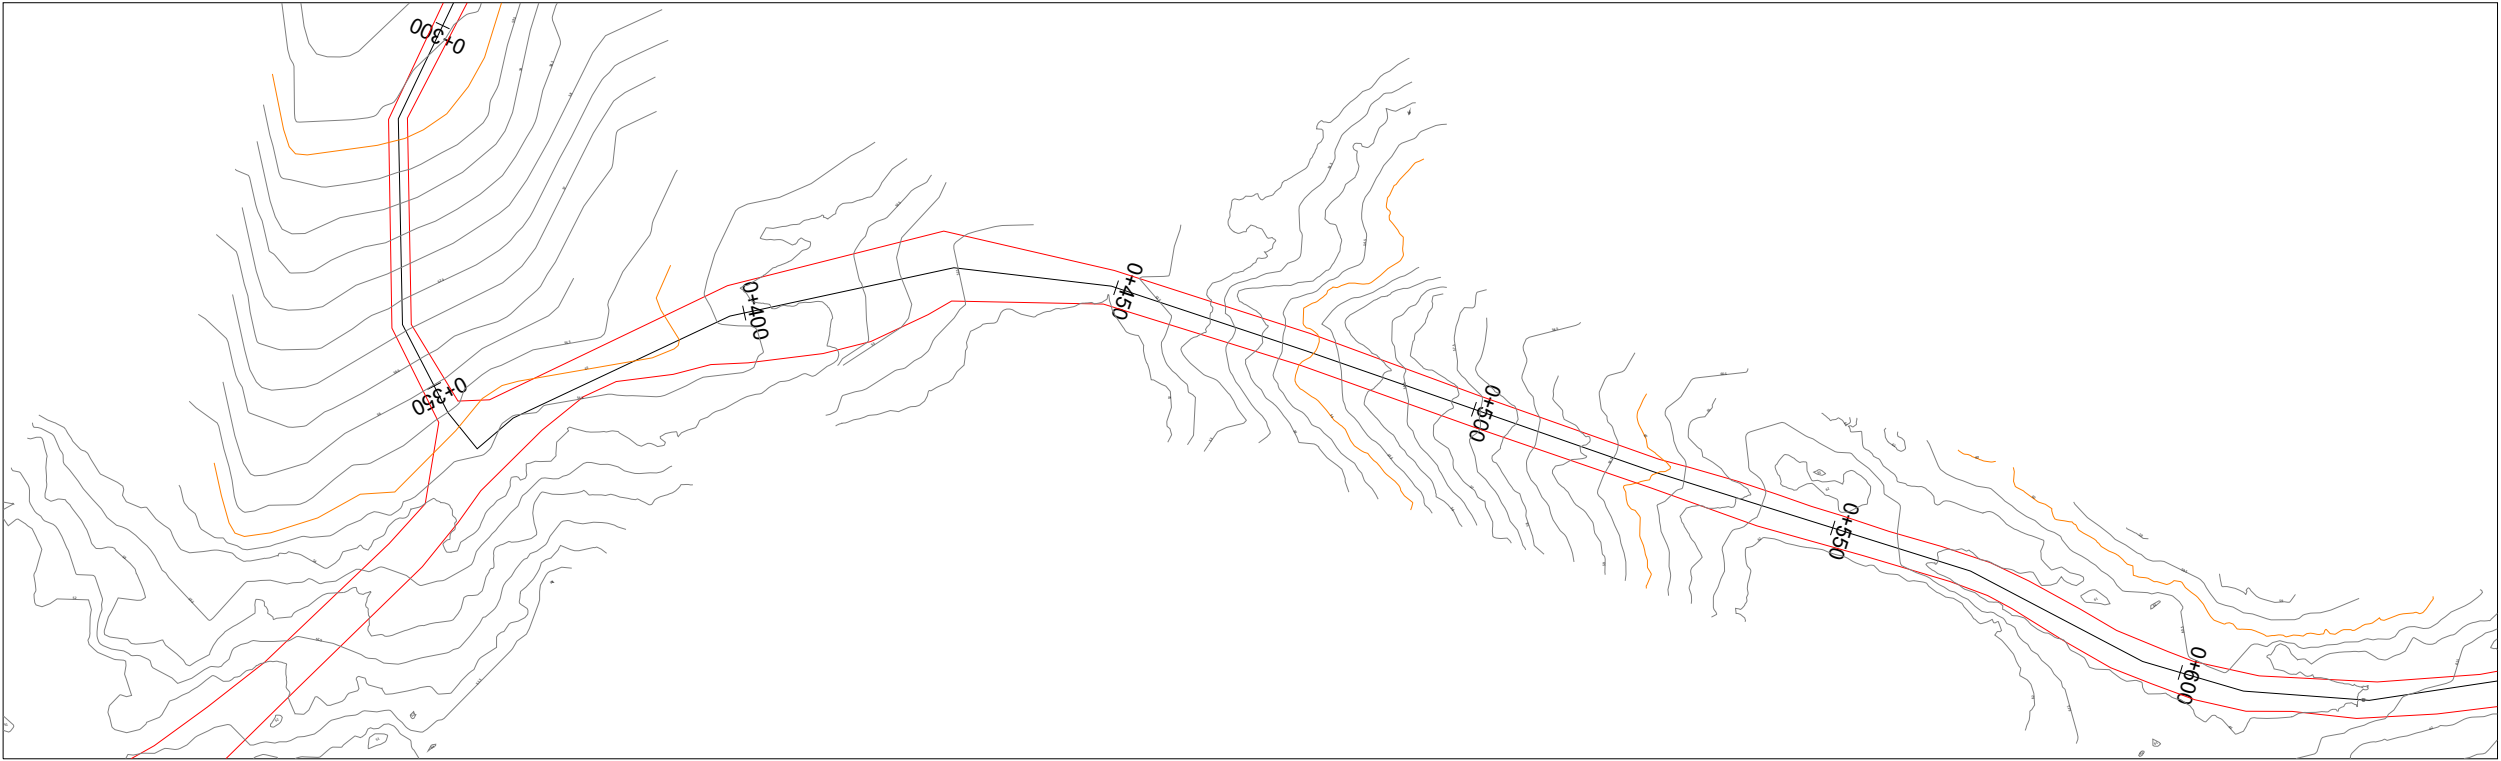


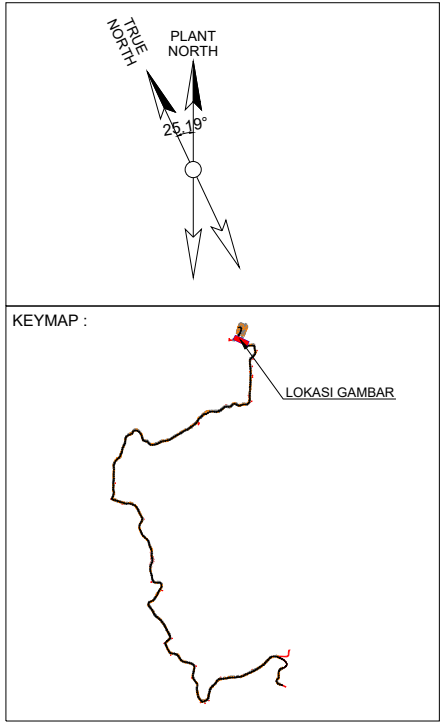

NOTES

1. ALL DIMENSIONS ARE MEASURED IN METER

LEGEND

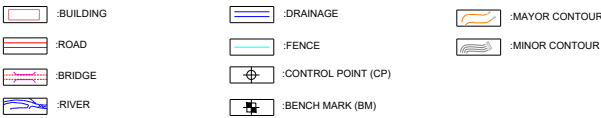

REFERENCE DWG NO.

TITLE

REV. NO.

DATE

DESCRIPTION

DRWN

CHK'D

APP'D

APP'D

OWNER:



CONSULTANT:



PROJECT TITLE :

Survey Pemetaan, Desain Siteplan Lokasi Bor CLA-001

DOC. NO. :

CONTRACT NO. : 4710001475

TITLE :

PETA SITUASI DAN CROSS SECTION

SCALE

1 : 1,000
1 : 200

DRAWING NO.

-

REV.

0

SIZE

A3