

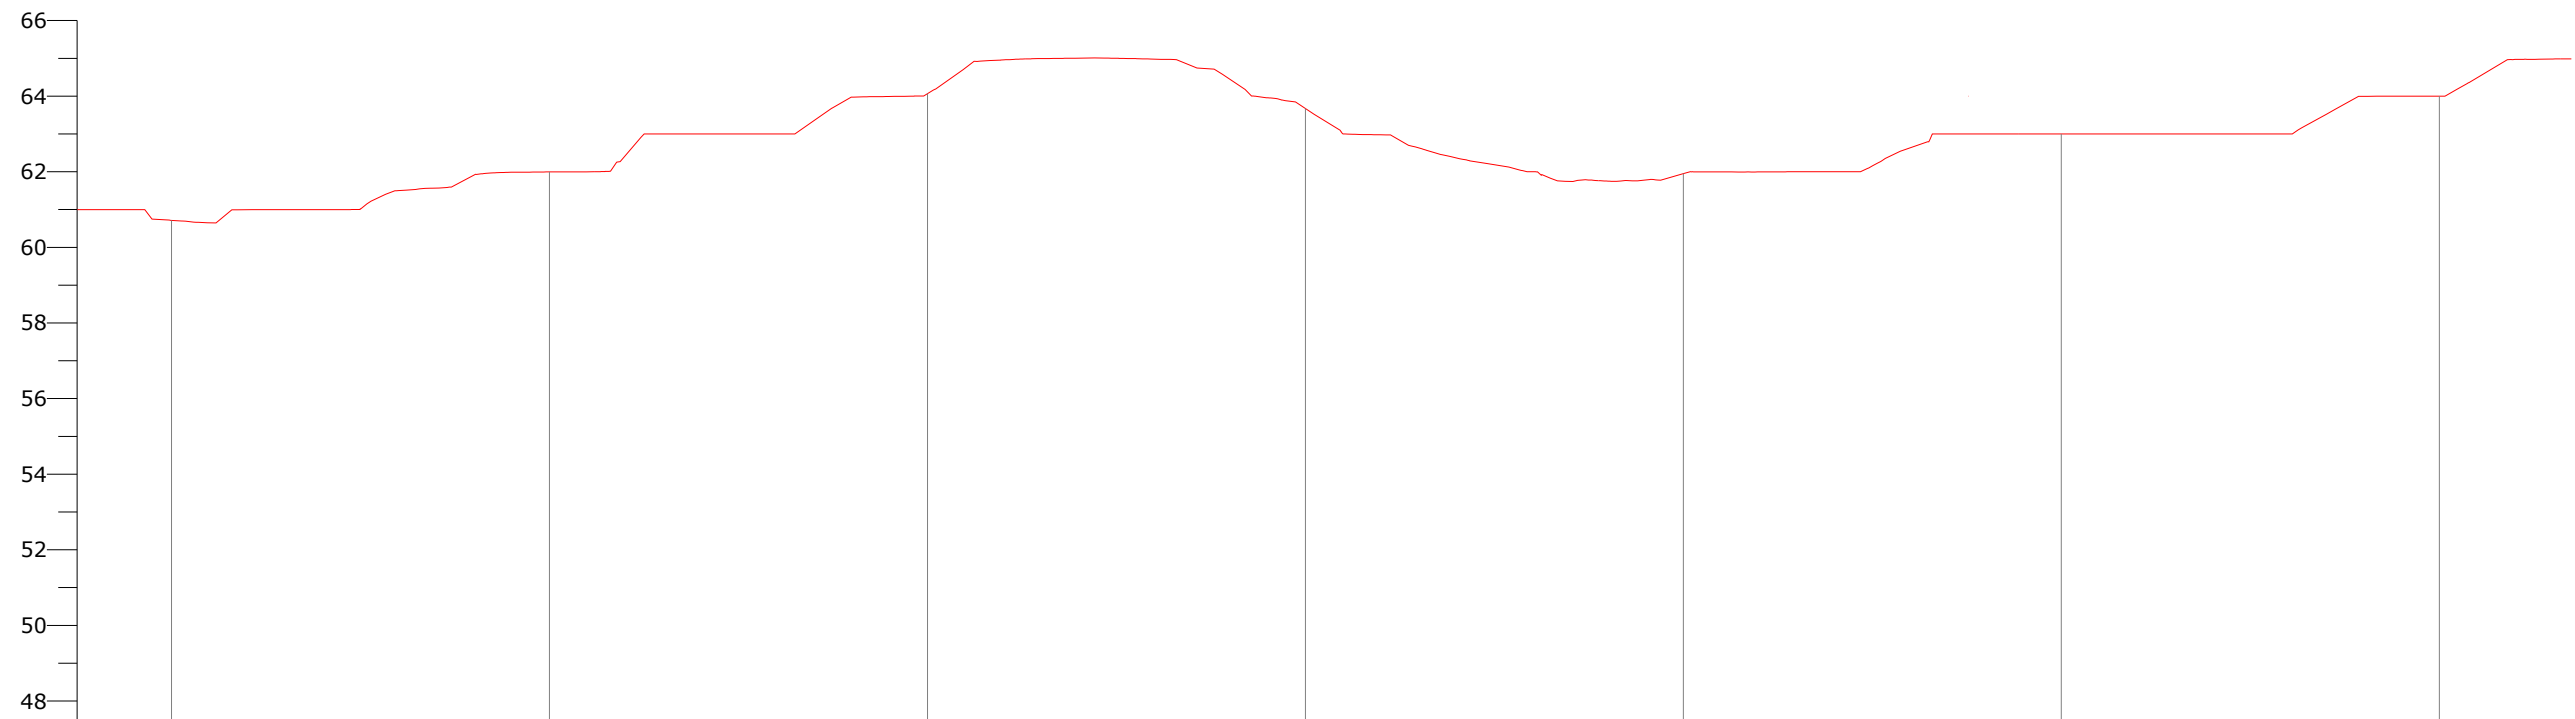
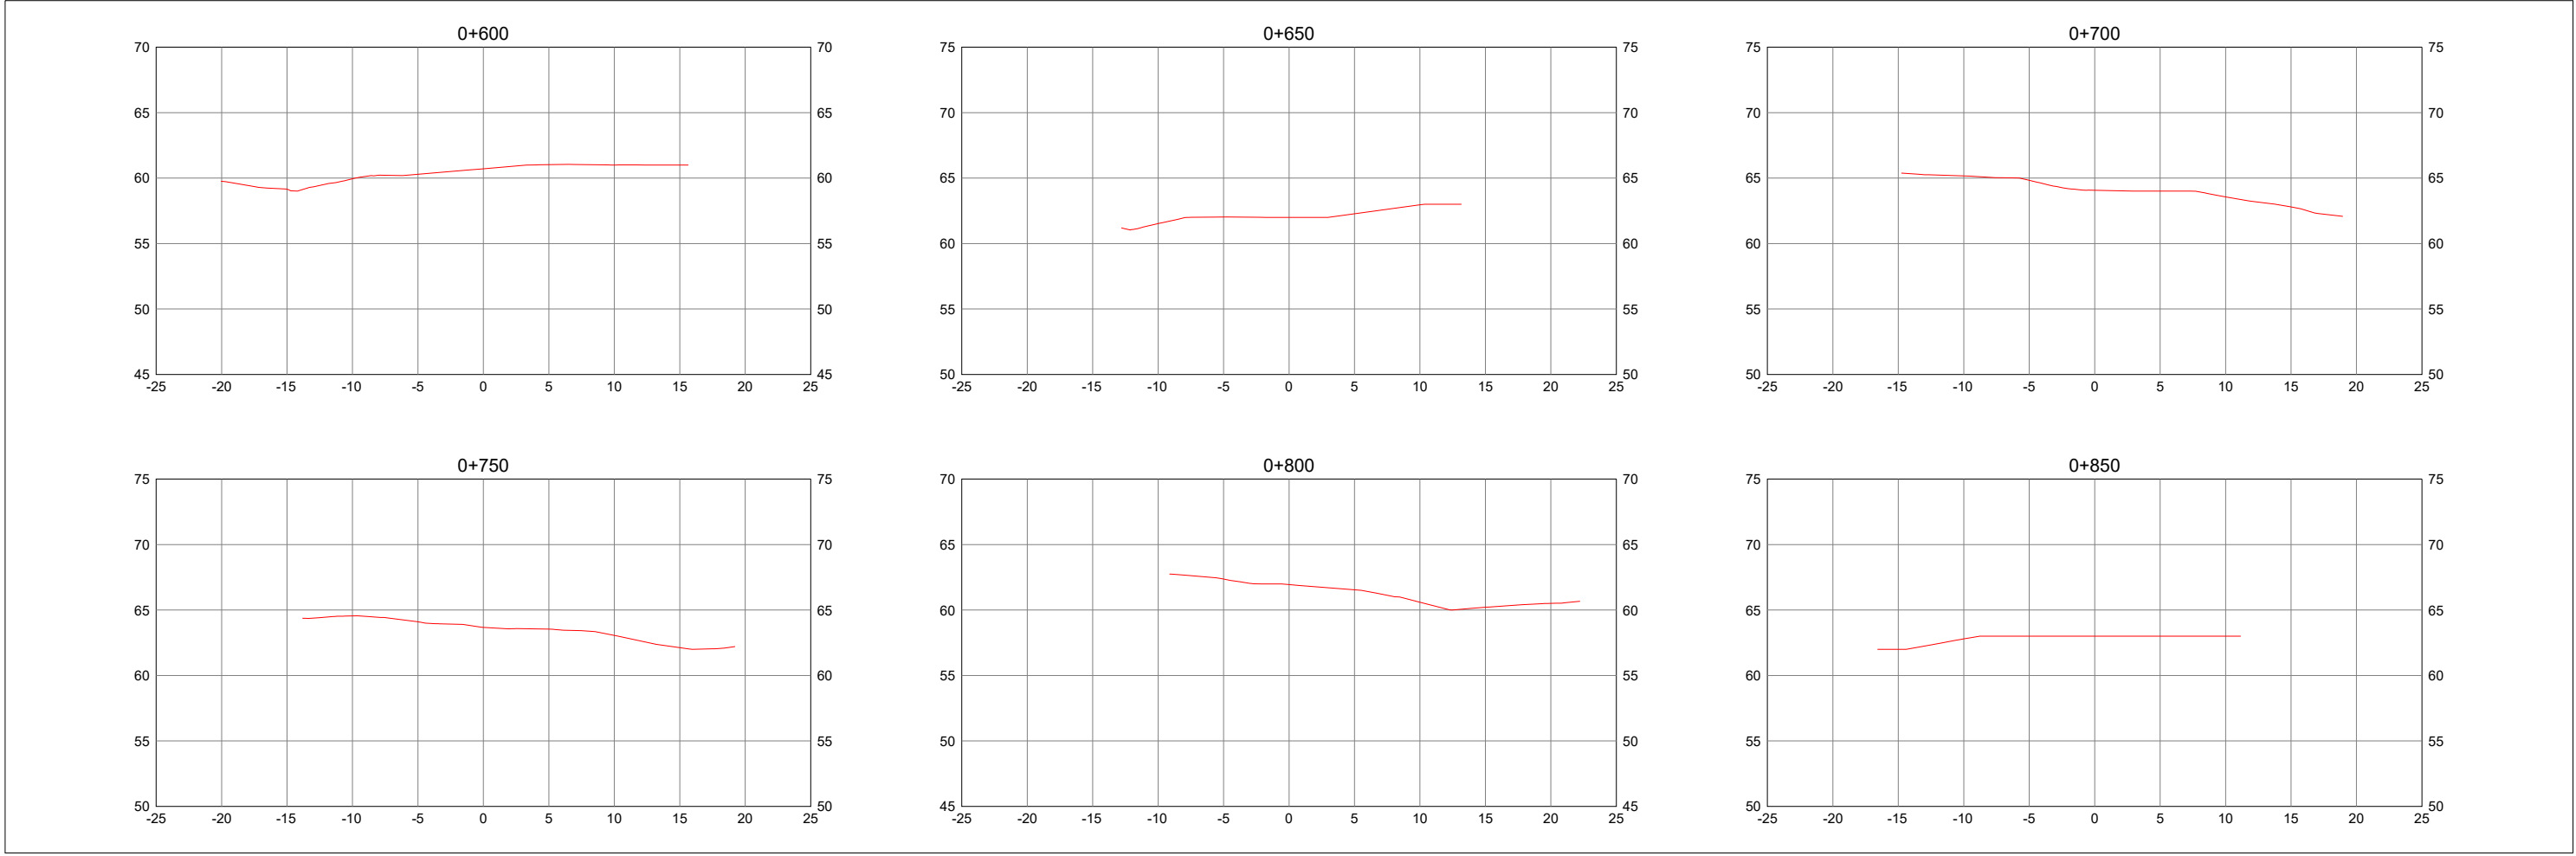


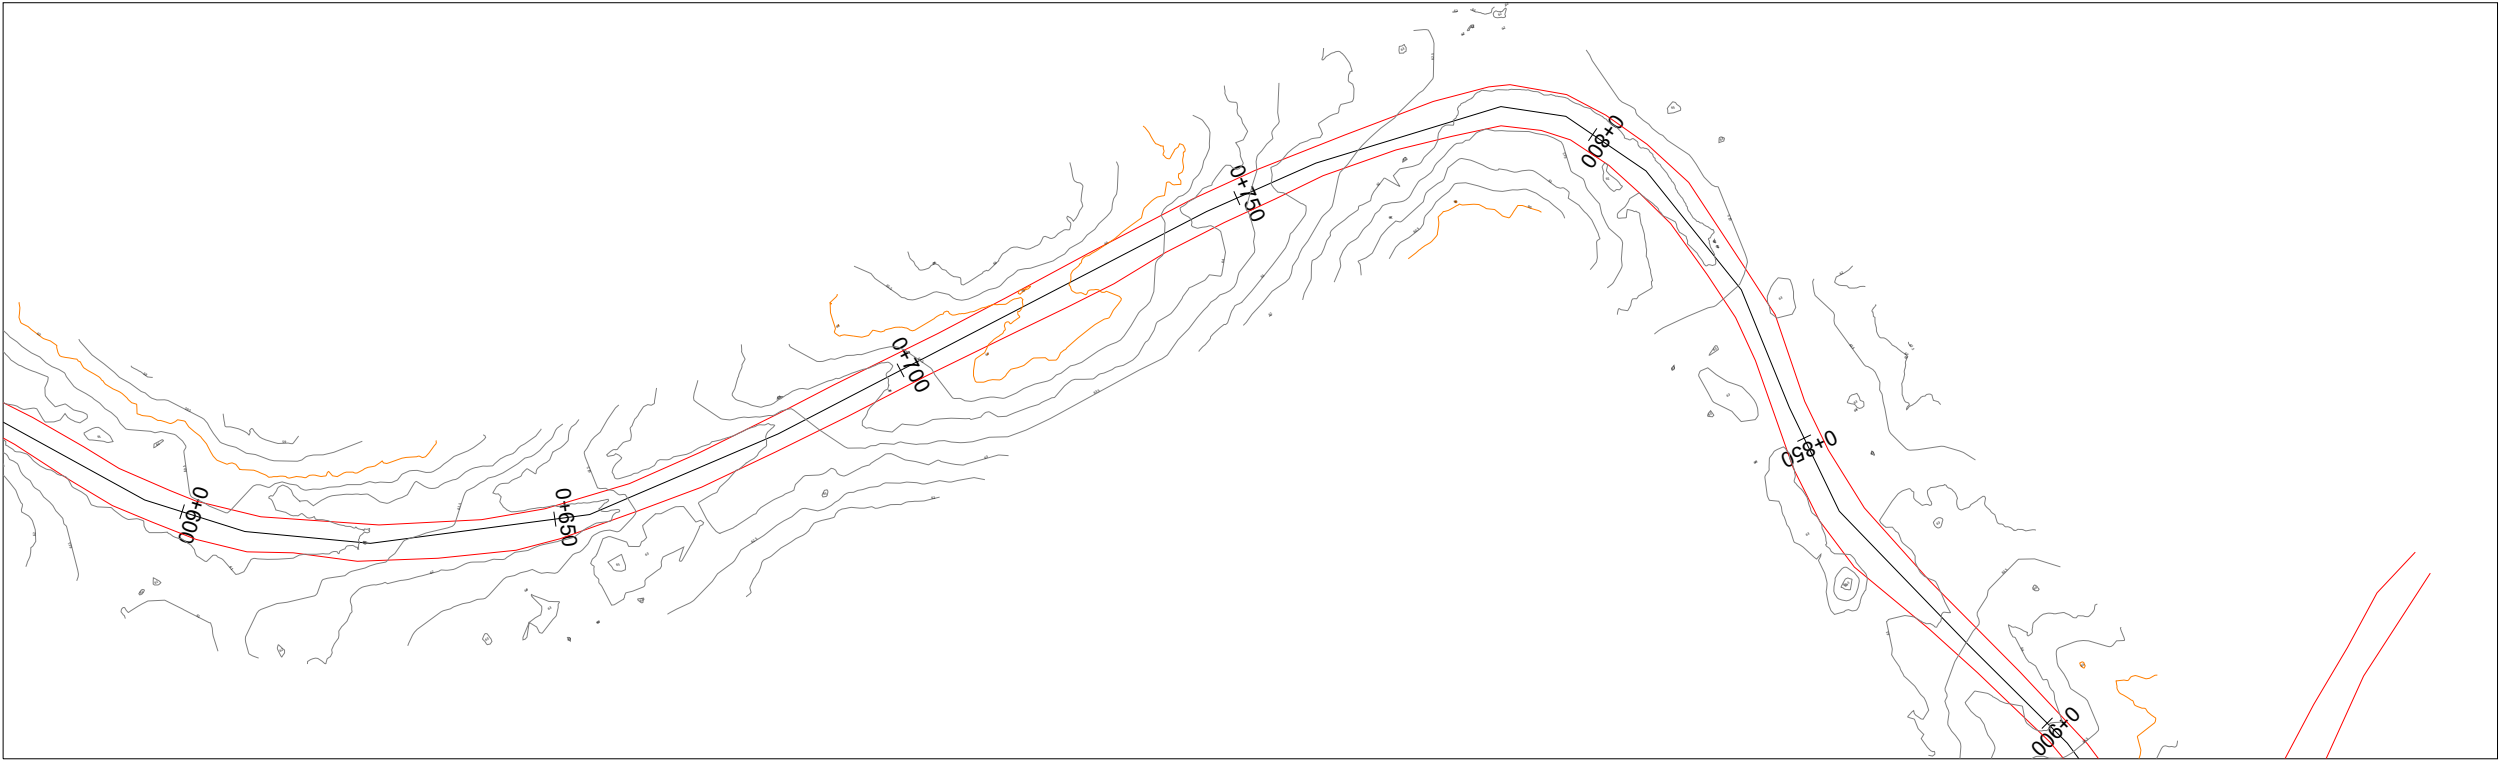

DATUM 46.00									
STA	0+600	0+650	0+700	0+750	0+800	0+850	0+900		
ELEVASI TANAH ASLI	60.712	61.995	64.065	63.672	61.950	63.000	64.000		
ELEVASI DESAIN									


NOTES	OWNER:										PROJECT TITLE :	
1. ALL DIMENSIONS ARE MEASURED IN METER	skkmigas																				Survey Pemetaan, Desain Siteplan Lokasi Bor CLA-001	
	DOC. NO. :										CONTRACT NO. : 4710001475	
LEGEND	

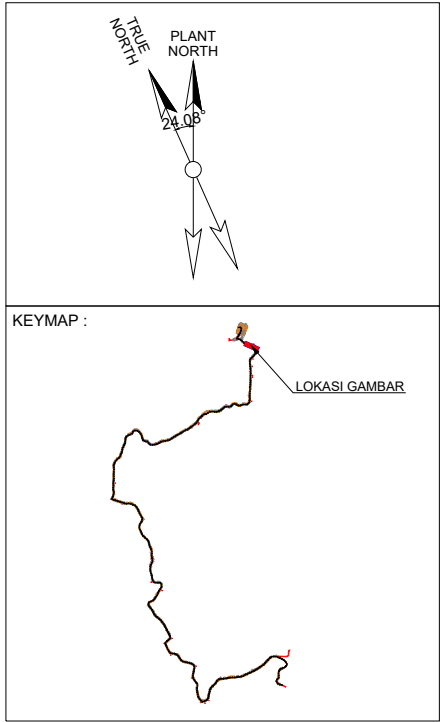

NOTES

1. ALL DIMENSIONS ARE MEASURED IN METER

LEGEND

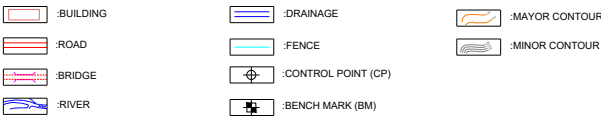

REFERENCE DWG NO.

TITLE

REV. NO.

DATE

DESCRIPTION

DRWN

CHK'D

APP'D

APP'D

OWNER:



CONSULTANT:



PROJECT TITLE :

Survey Pemetaan, Desain Siteplan Lokasi Bor CLA-001

DOC. NO. :

CONTRACT NO. : 4710001475

TITLE :

PETA SITUASI DAN CROSS SECTION

SCALE

1 : 1,000
1 : 200

DRAWING NO.

-

REV.

0

SIZE

A3