
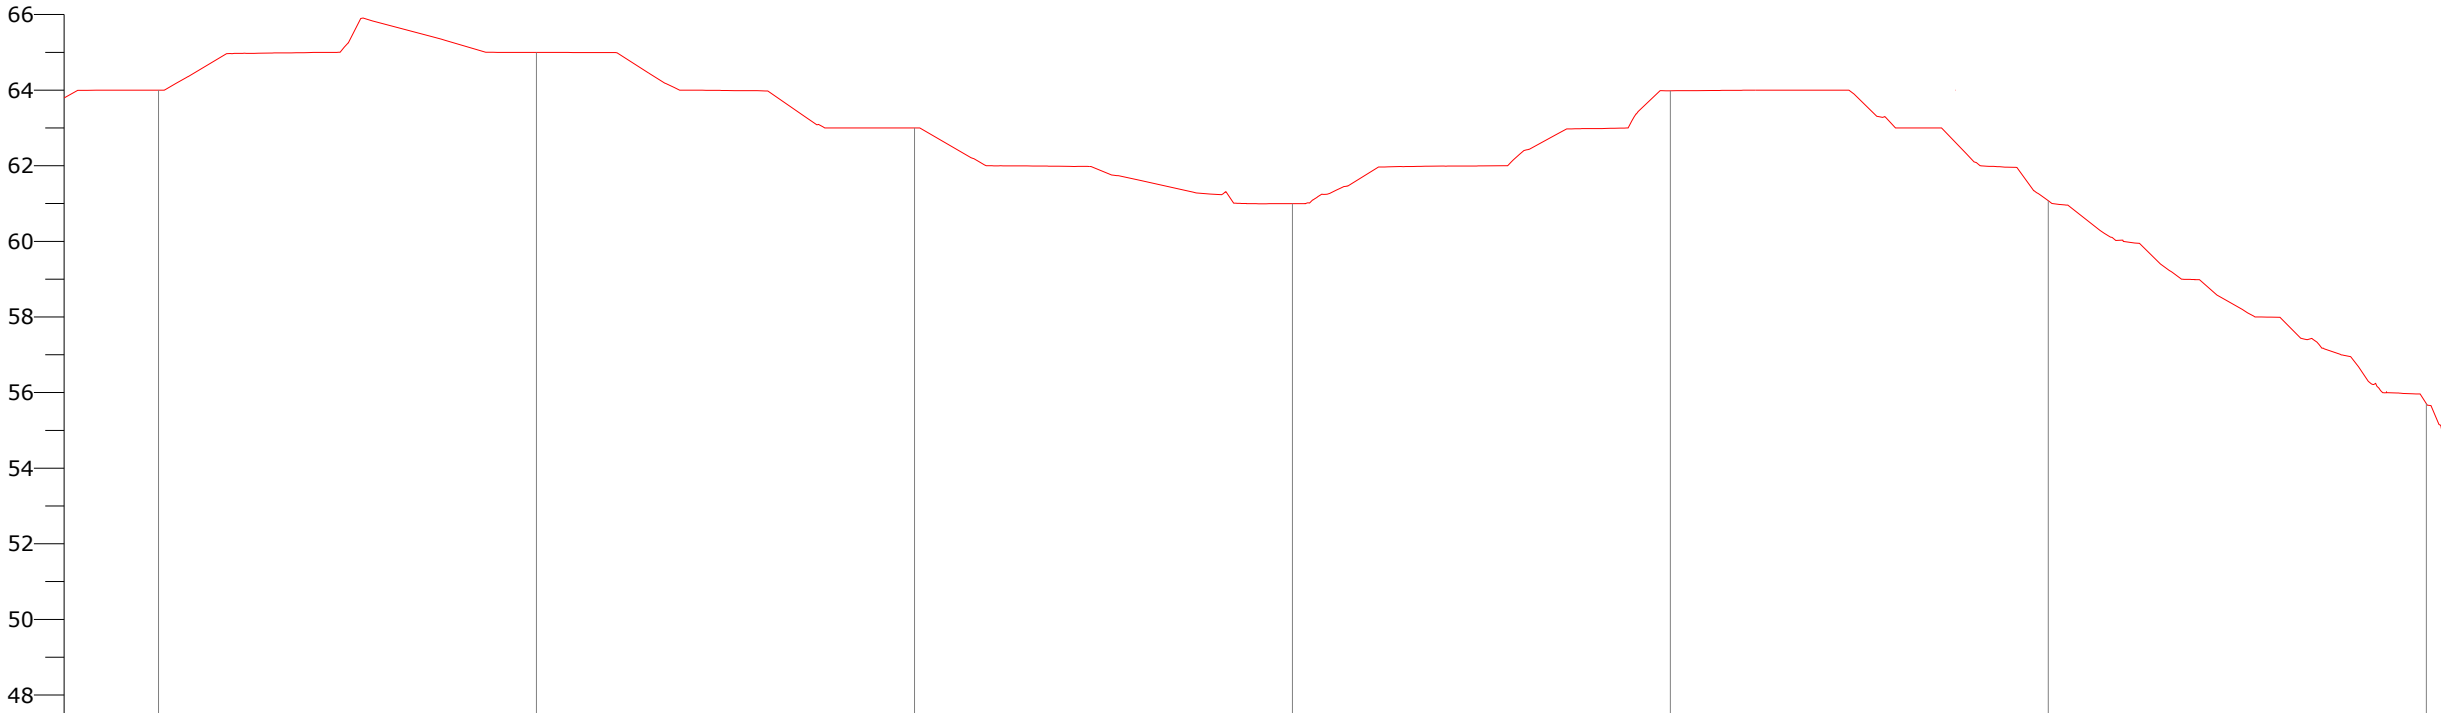
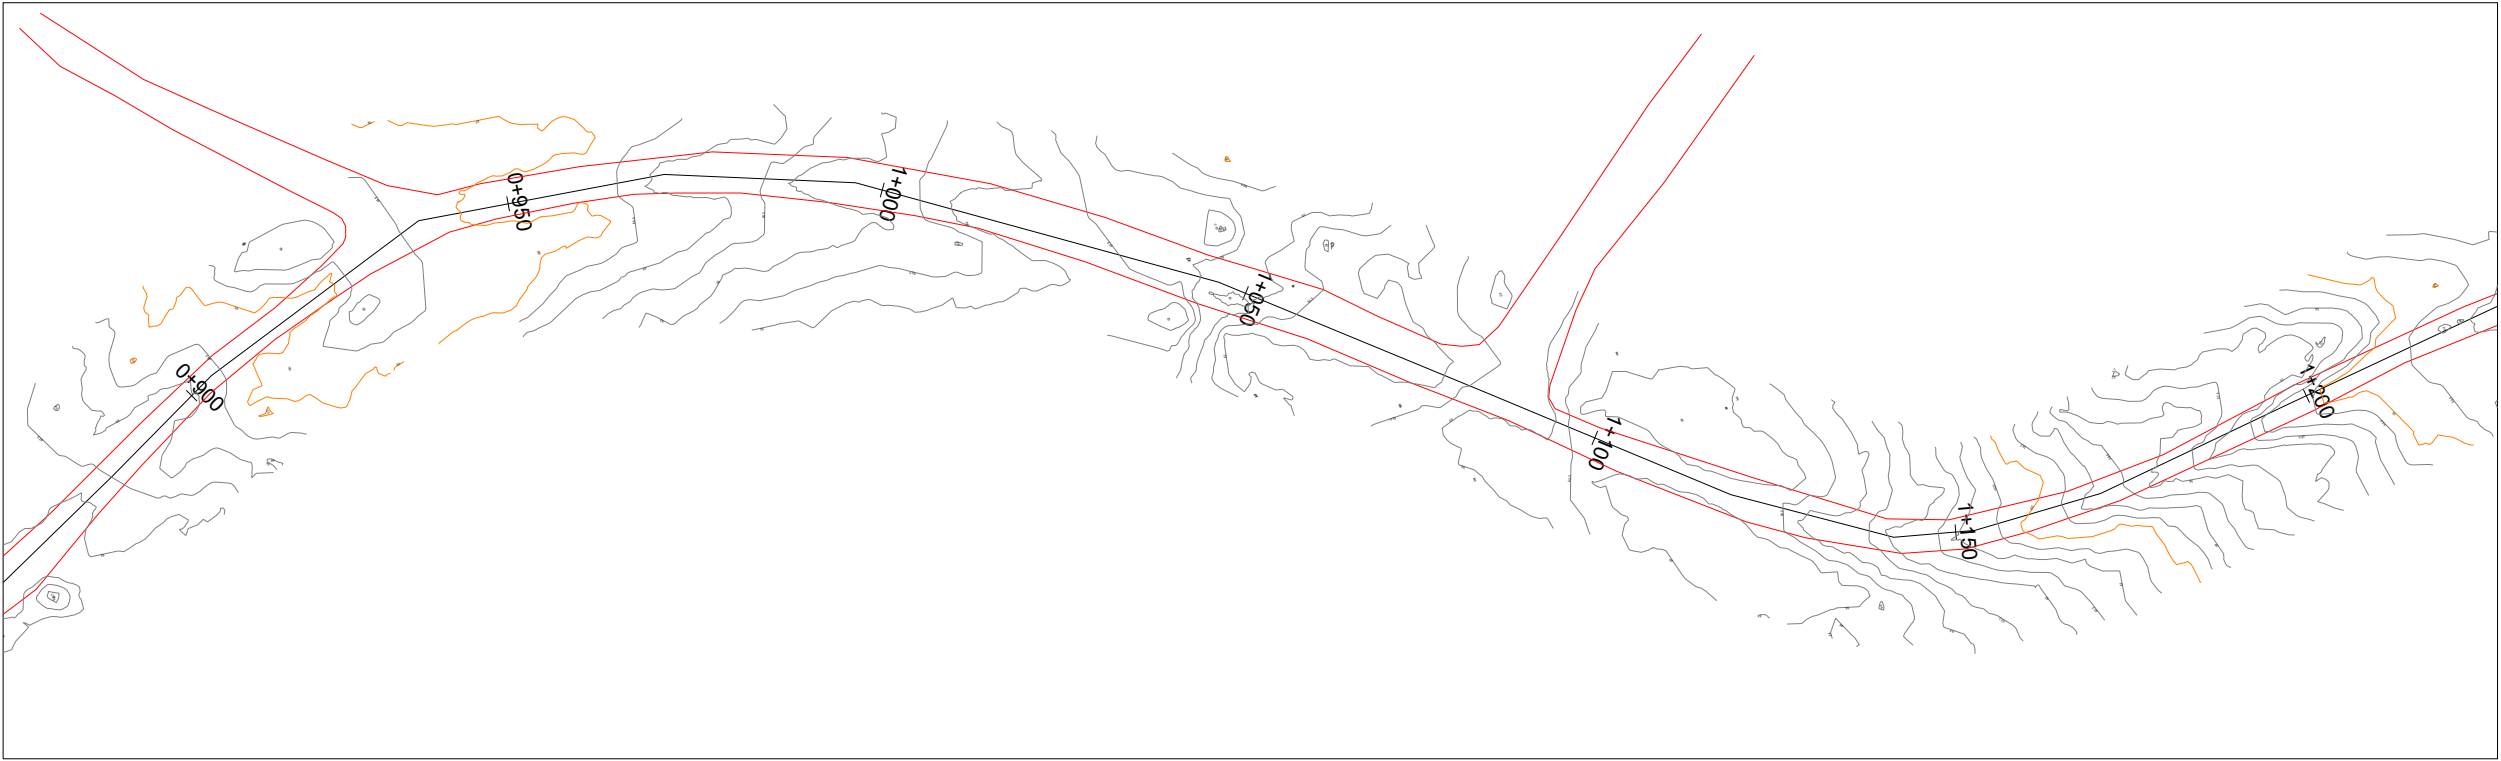


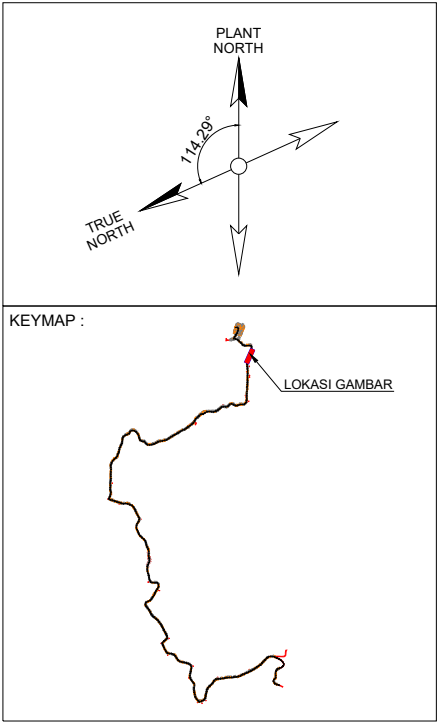

STA	0+900	0+950	1+000	1+050	1+100	1+150	1+200
ELEVASI TANAH ASLI	64.000	64.998	62.998	60.998	63.983	61.074	55.712
ELEVASI DESAIN							

NOTES

1. ALL DIMENSIONS ARE MEASURED IN METER

LEGEND

BUILDING

ROAD

BRIDGE

RIVER

DRAINAGE

FENCE

CONTROL POINT (CP)

BENCH MARK (BM)

MAJOR CONTOUR

MINOR CONTOUR

REFERENCE DWG NO.

TITLE

REV. NO.

DATE

DESCRIPTION

DRWN

CHK'D

APP'D

APP'D

OWNER:

skkmigas

PERTAMINA

EP

CONSULTANT:

SUCOFINDO

PROJECT TITLE :

Survey Pemetaan, Desain Siteplan Lokasi Bor CLA-001

DOC. NO. :

CONTRACT NO. : 4710001475

TITLE :

PETA SITUASI DAN LONG SECTION

SCALE

1 : 1.000

1 : 200

DRAWING NO.




-

REV.

0

SIZE

A3

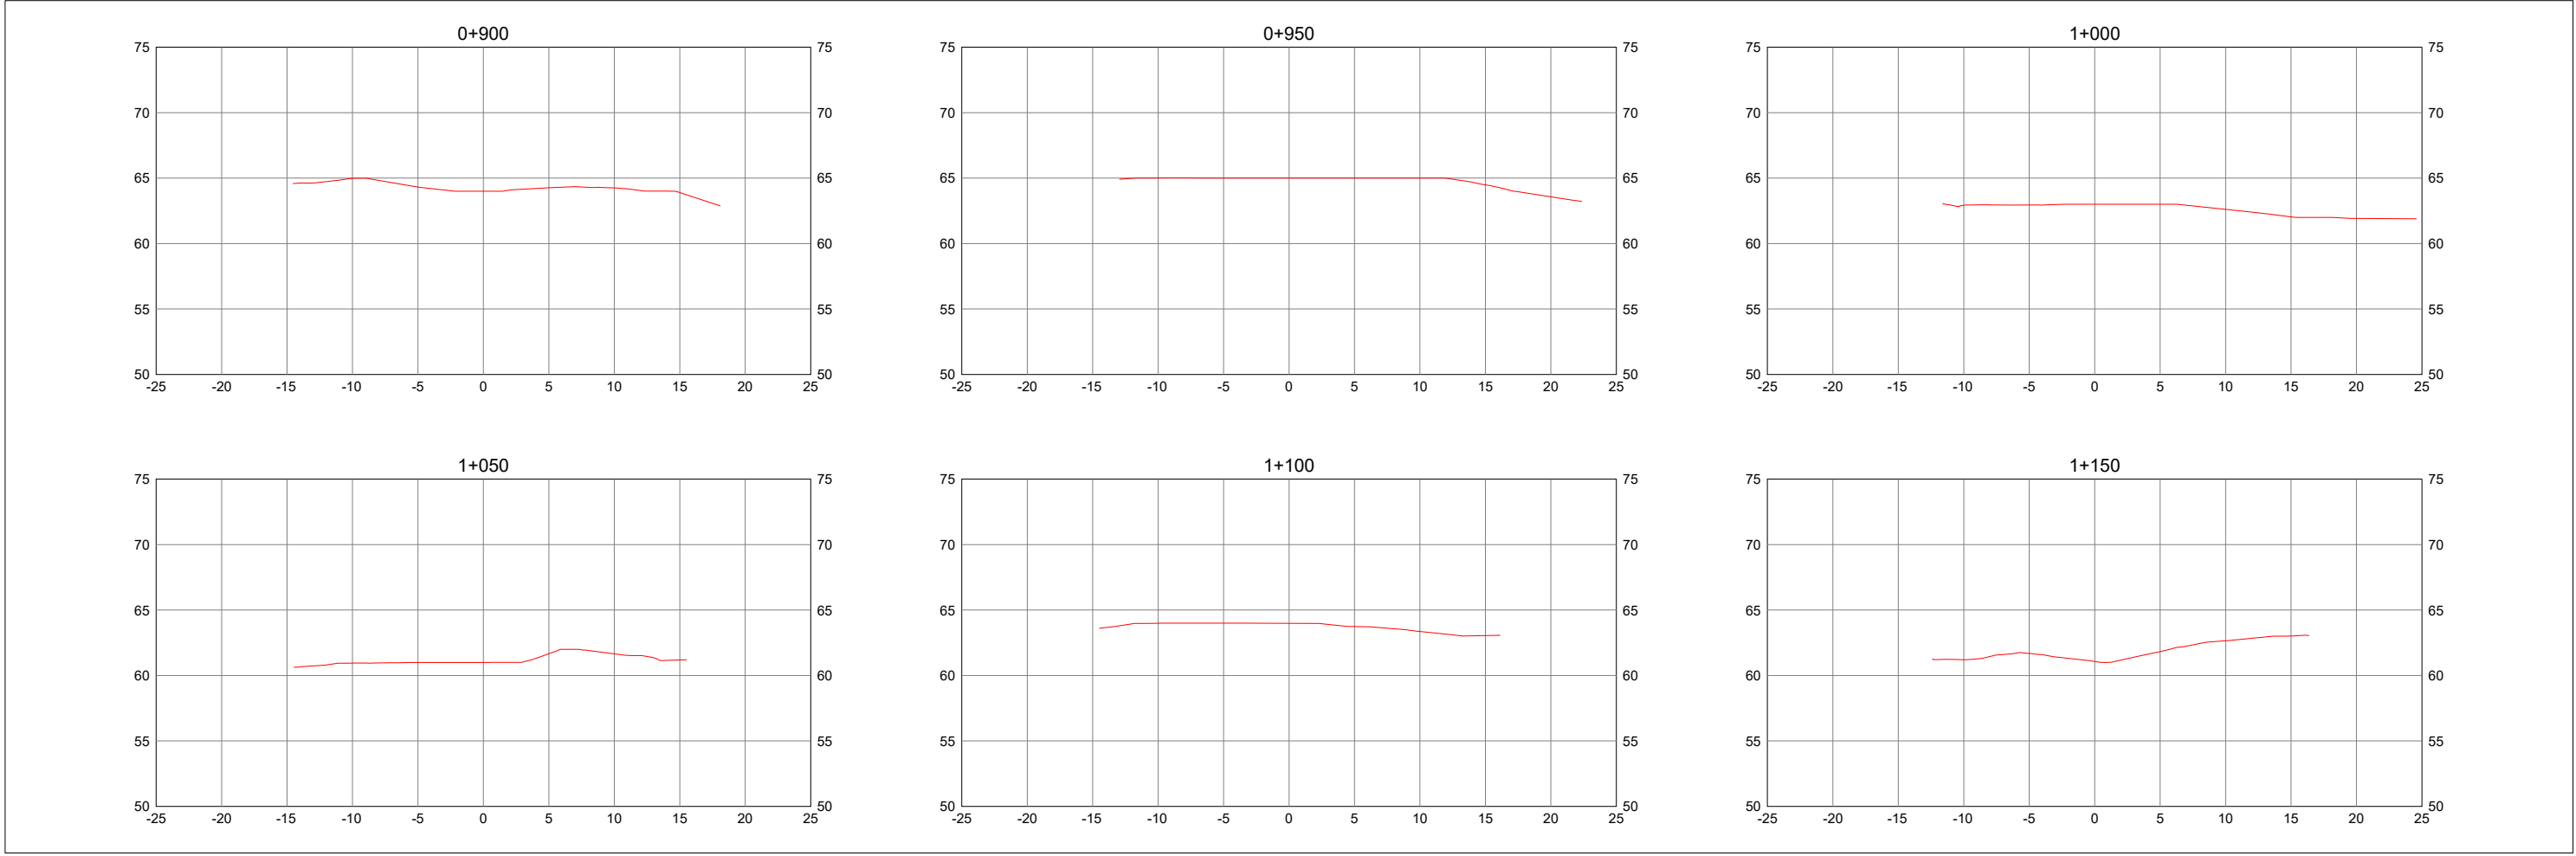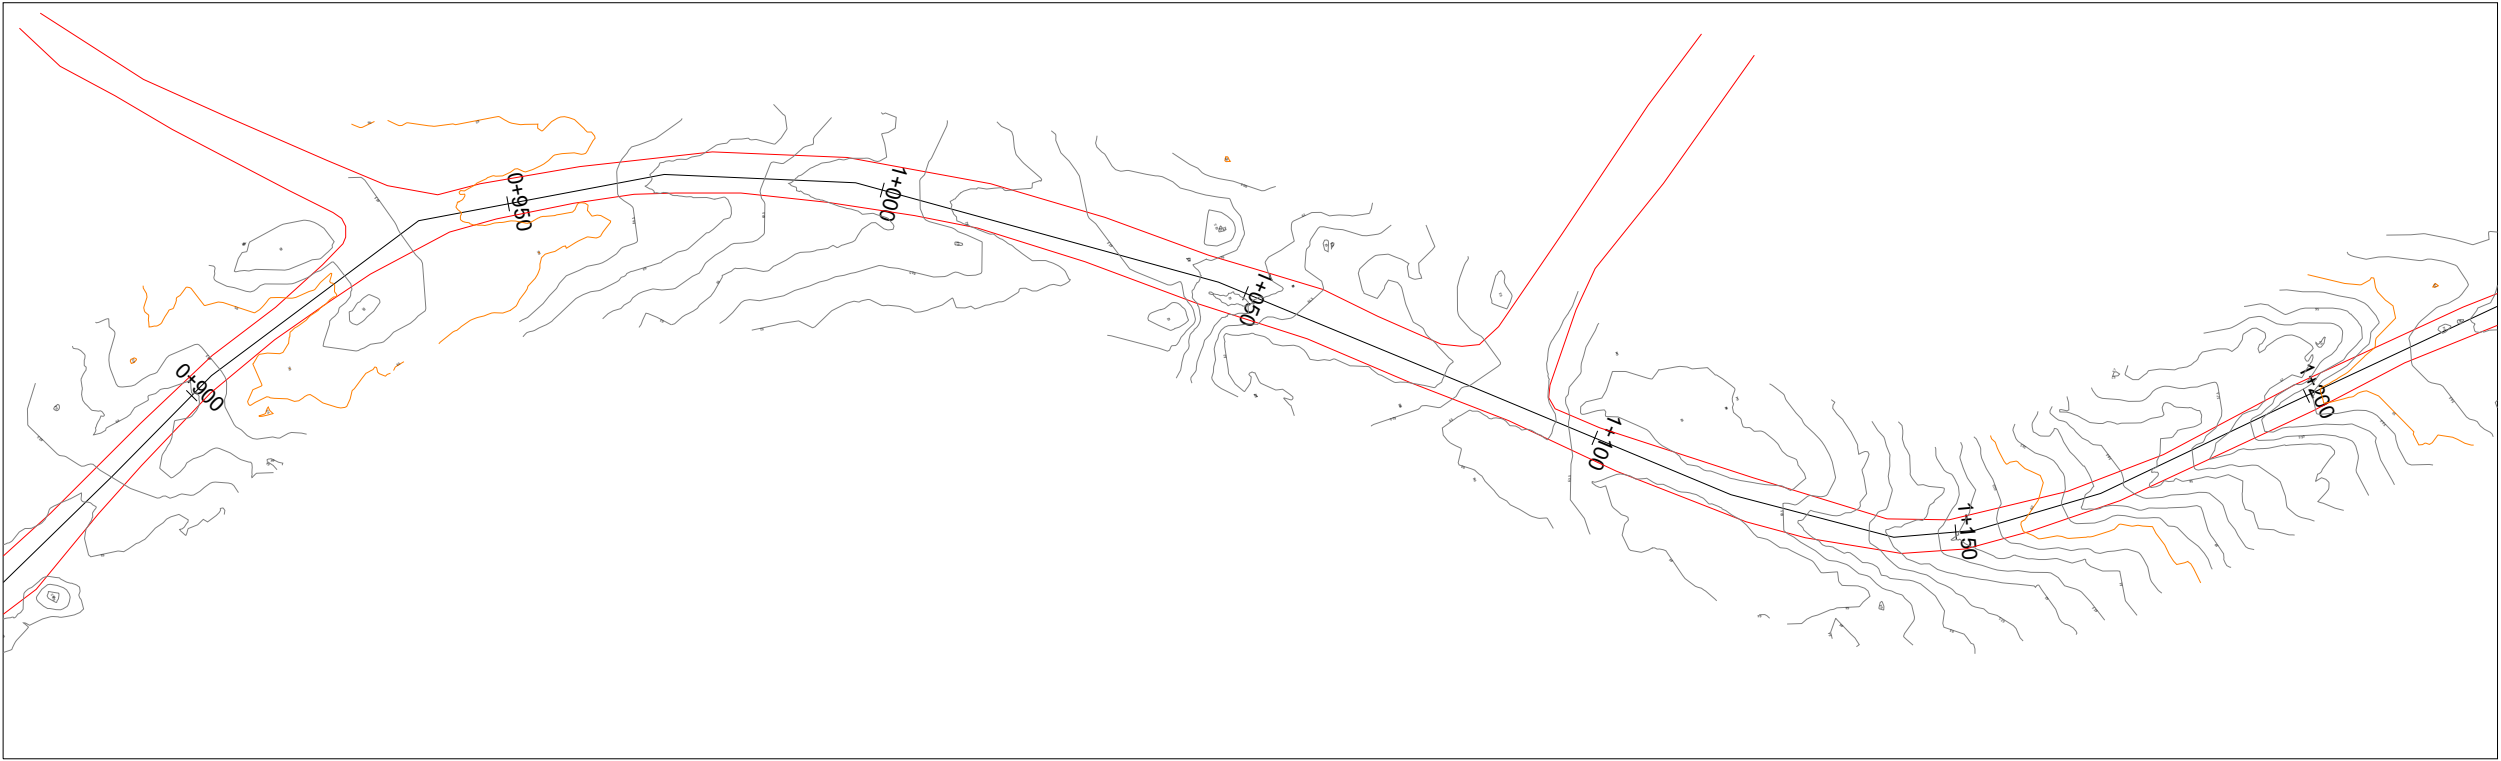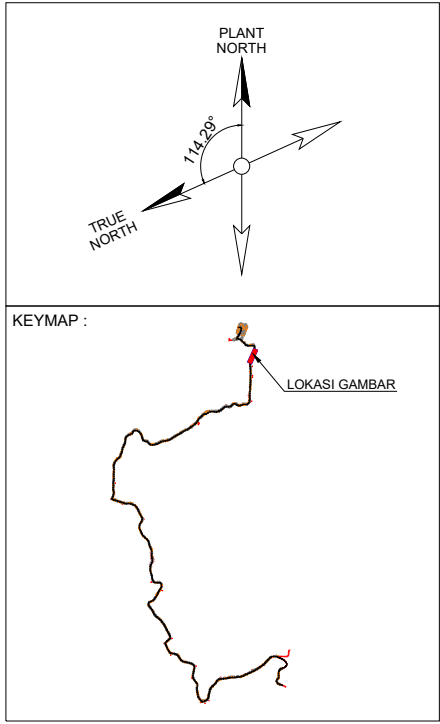

NOTES

1. ALL DIMENSIONS ARE MEASURED IN METER

LEGEND

	BUILDING		DRAINAGE		MAJOR CONTOUR
	ROAD		FENCE		MINOR CONTOUR
	BRIDGE		CONTROL POINT (CP)		
	RIVER		BENCH MARK (BM)		

REFERENCE DWG NO.

TITLE

REV. NO.

DATE

DESCRIPTION

DRWN

CHK'D

APP'D

APP'D

OWNER:



CONSULTANT:



PROJECT TITLE :

Survey Pemetaan, Desain Siteplan Lokasi Bor CLA-001

DOC. NO. :

CONTRACT NO. : 4710001475

TITLE :

PETA SITUASI DAN CROSS SECTION

SCALE

1 : 1.000
1 : 200

DRAWING NO.

-

REV.

0

SIZE

A3