
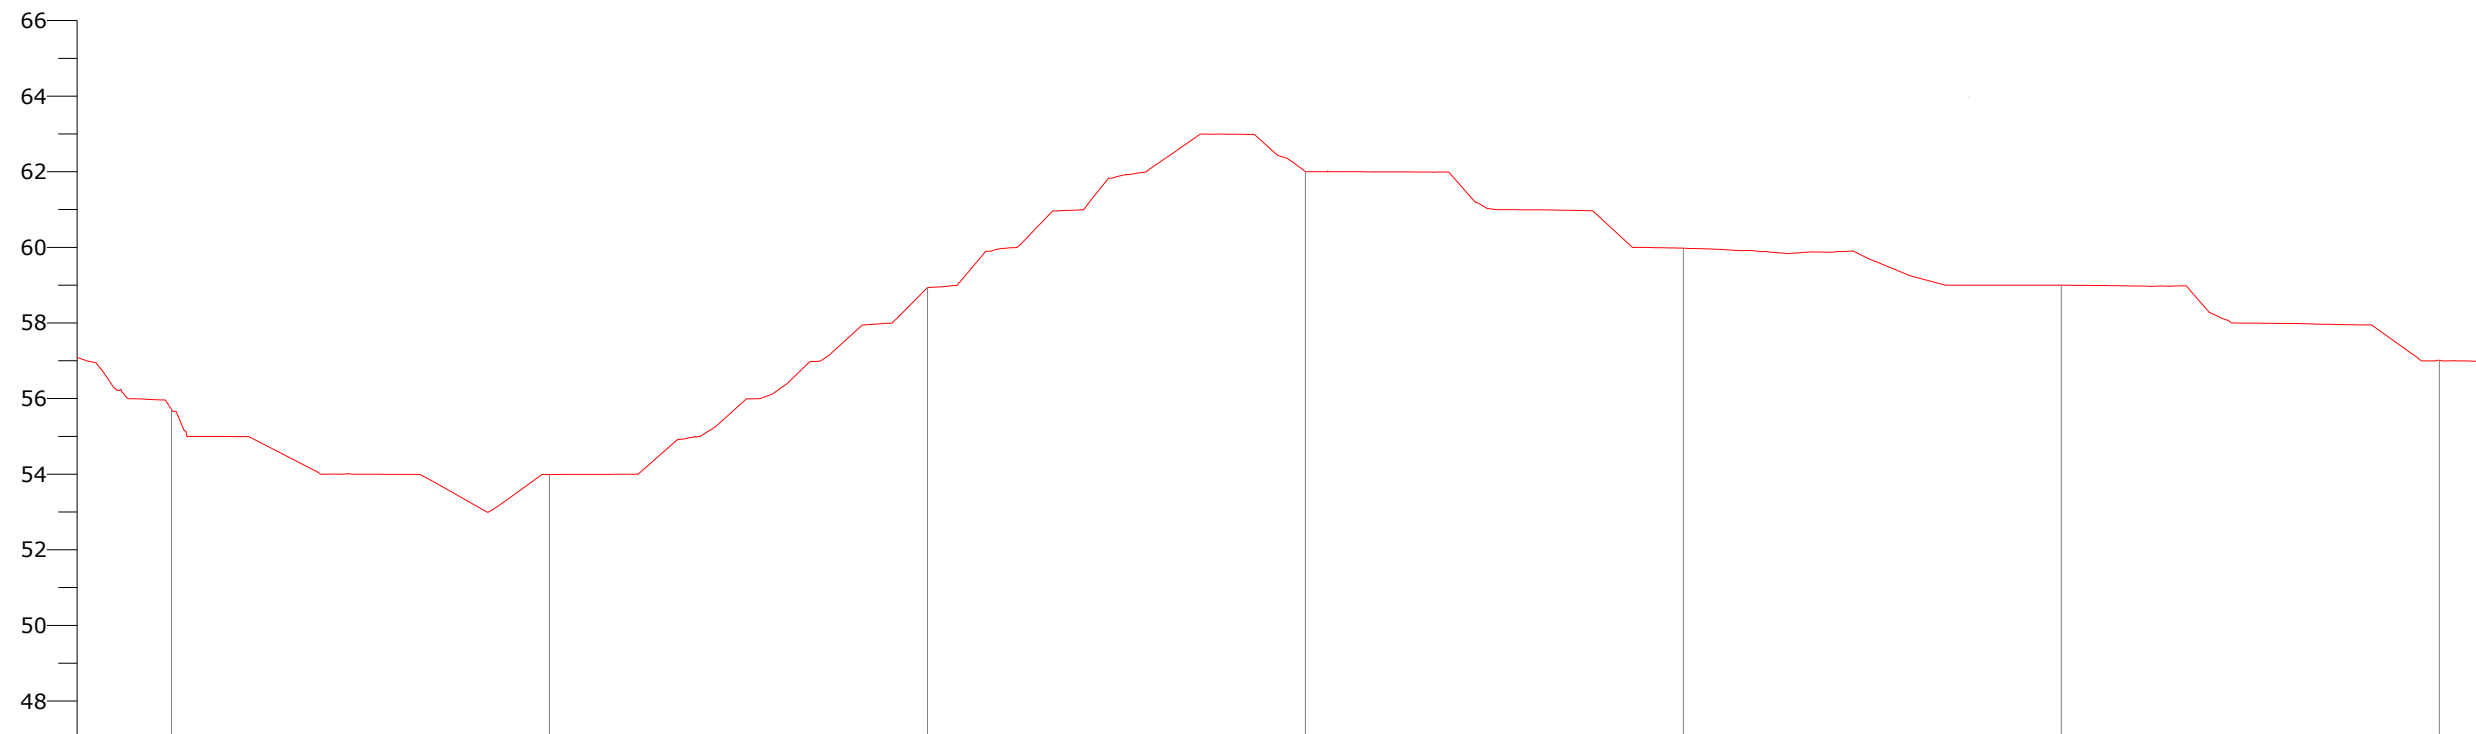


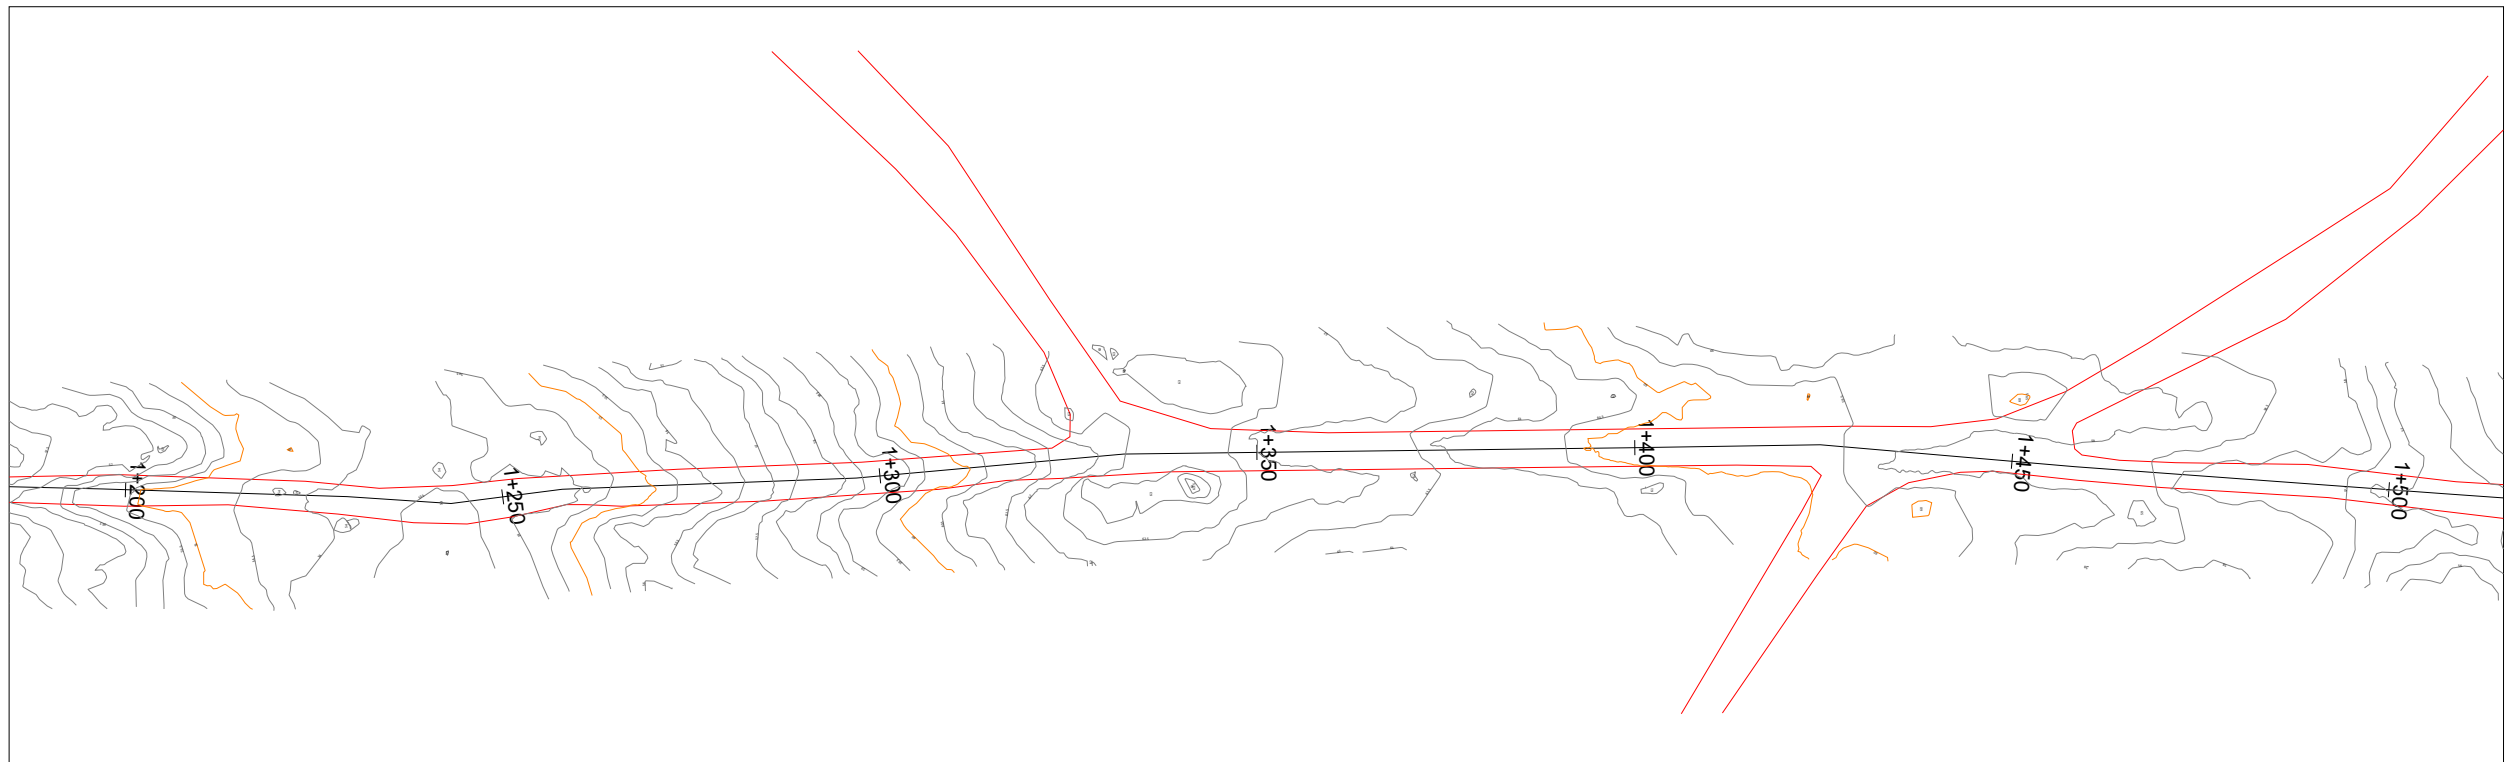

DATUM 46.00							
STA	1+200	1+250	1+300	1+350	1+400	1+450	1+500
ELEVASI TANAH ASLI	55.712	53.993	58.943	62.009	59.977	58.999	57.014
ELEVASI DESAIN							

1. ALL DIMENSIONS ARE MEASURED IN METER

	:BUILDING		:DRAINAGE		:MAYOR CONTOUR
	:ROAD		:FENCE		:MINOR CONTOUR
	:BRIDGE		:CONTROL POINT (CP)		
	:RIVER		:BENCH MARK (BM)		



		△							
		△							
		△							
		△							
		△							
		△							
		△							
REFERENCE DWG NO.	TITLE	REV. NO.	DATE	DESCRIPTION	DRWN	CHK'D	APP'D	APP'D	

skkmigas 



SCALE
1 : 1.000
1 : 200

DRAWING NO.	REV.	5
-	0	

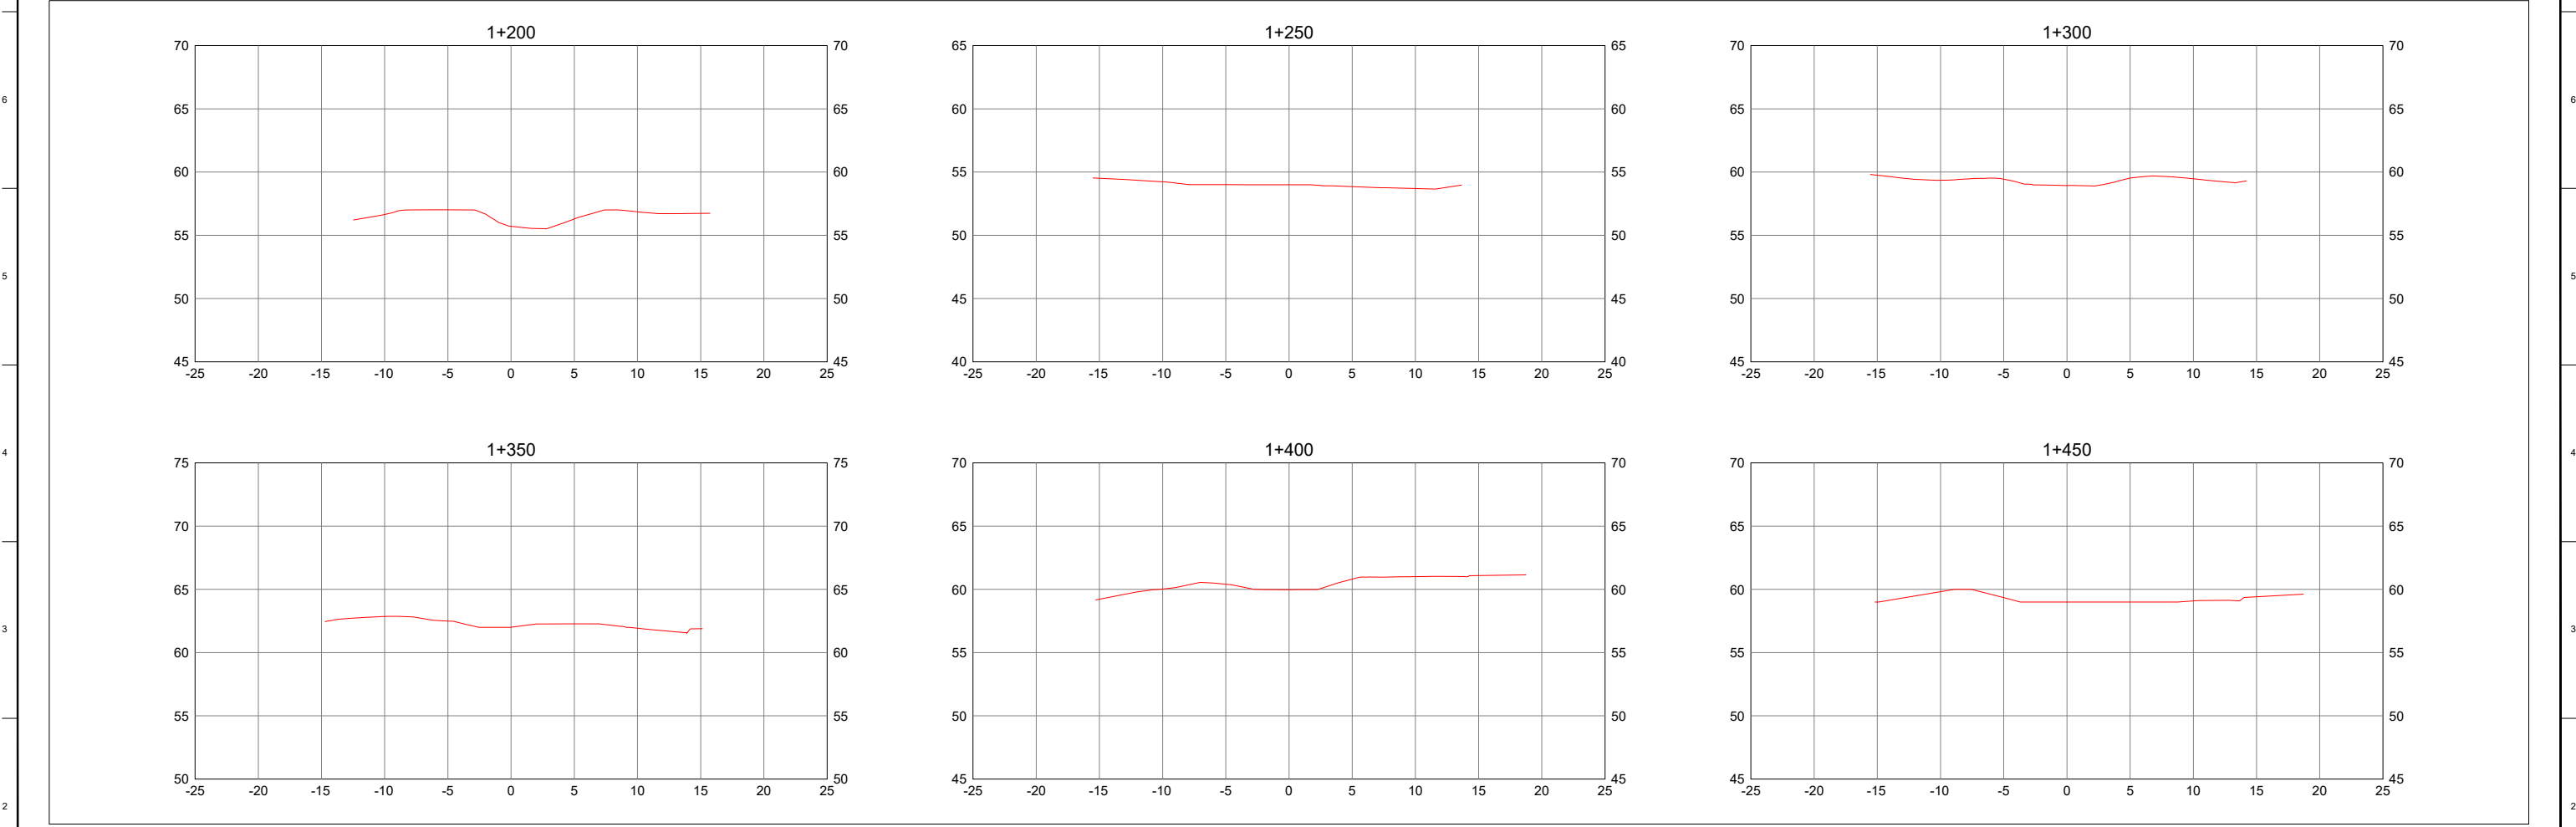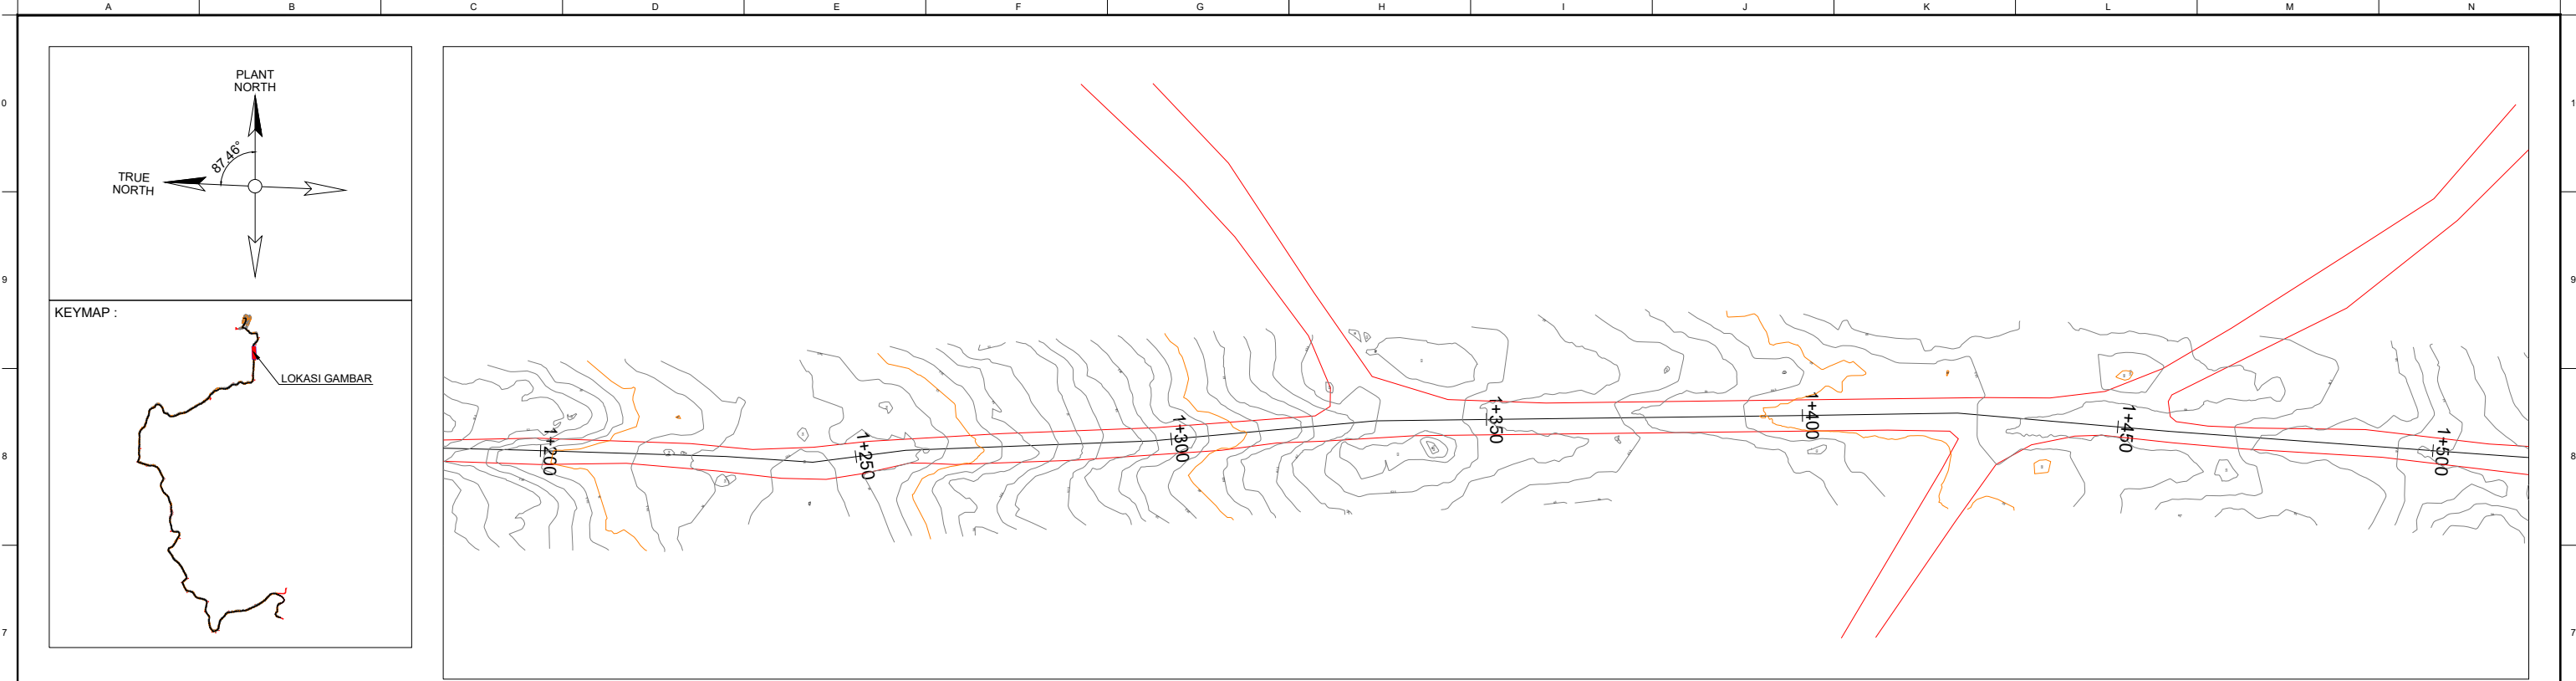

NOTES										OWNER:										PROJECT TITLE :																					
1. ALL DIMENSIONS ARE MEASURED IN METER										skkmigas PERTAMINA EP										Survey Pemetaan, Desain Siteplan Lokasi Bor CLA-001																					
LEGEND										CONSULTANT:										DOC. NO. : CONTRACT NO. : 4710001475																					
:BUILDING :DRAINAGE :MAYOR CONTOUR :ROAD :FENCE :MINOR CONTOUR :BRIDGE :CONTROL POINT (CP) :RIVER :BENCH MARK (BM)										SUCOFINDO										TITLE : PETA SITUASI DAN CROSS SECTION																					
REFERENCE DWG NO.										TITLE										REV. NO.		DATE		DESCRIPTION		DRWN		CHK'D		APP'D		APP'D		SCALE		DRAWING NO.		REV.		SIZE	
																																		1 : 1.000 1 : 200		-		0		A3	
A			B			C			D			E			F			G			H			I			J			K			L			M			N		