


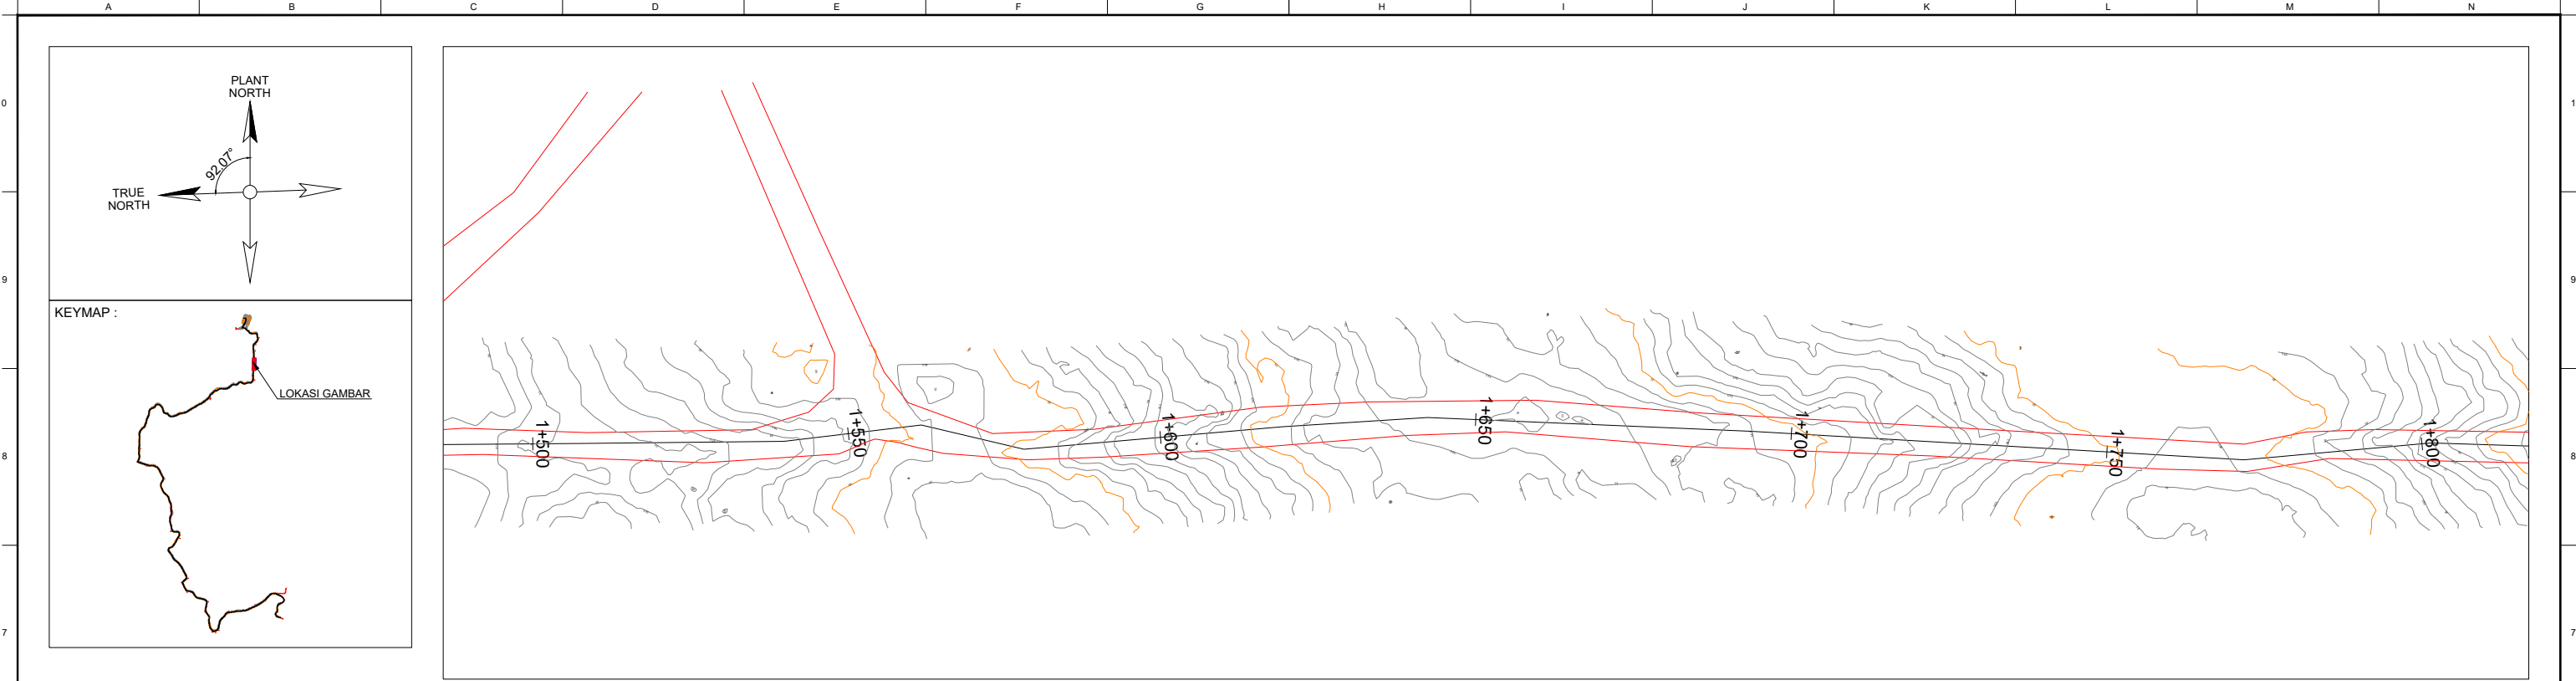
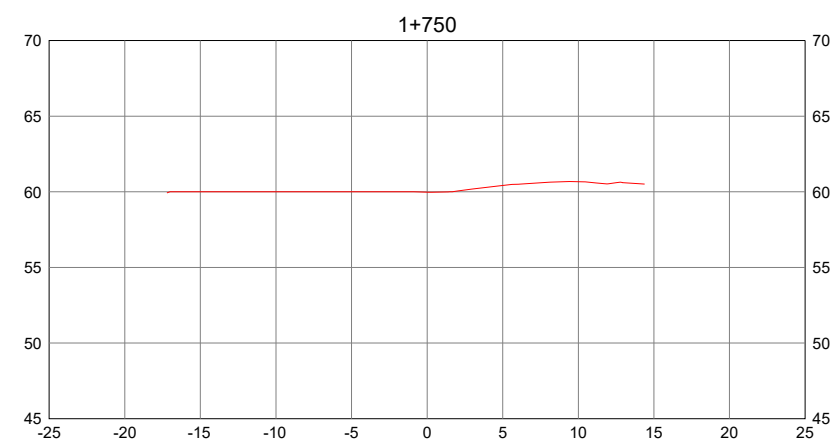
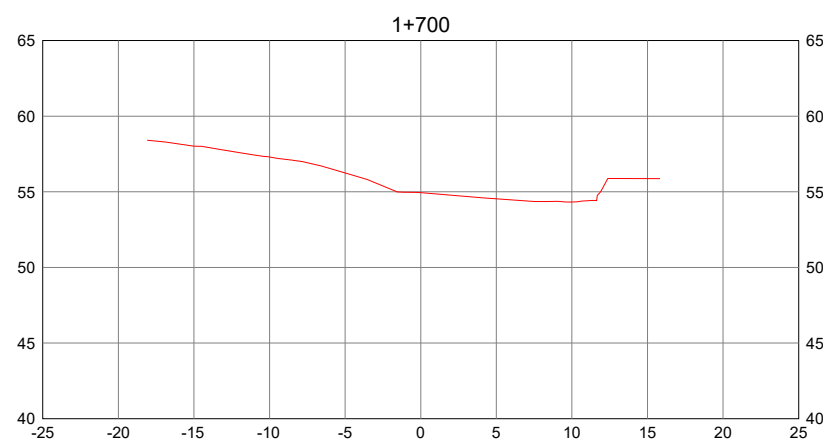
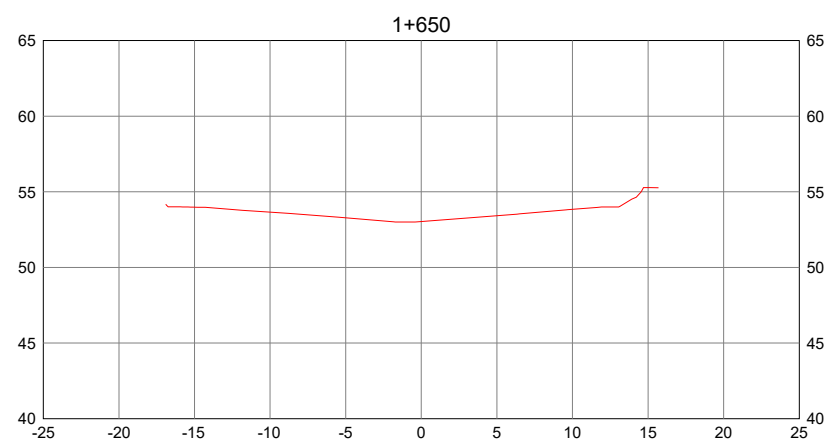
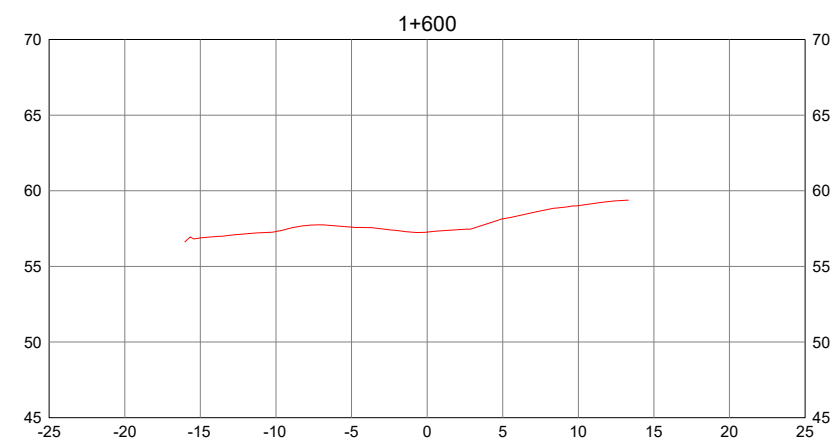


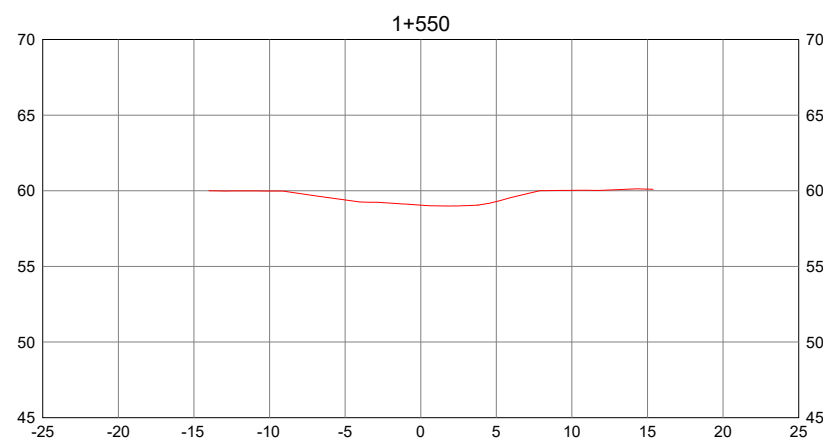

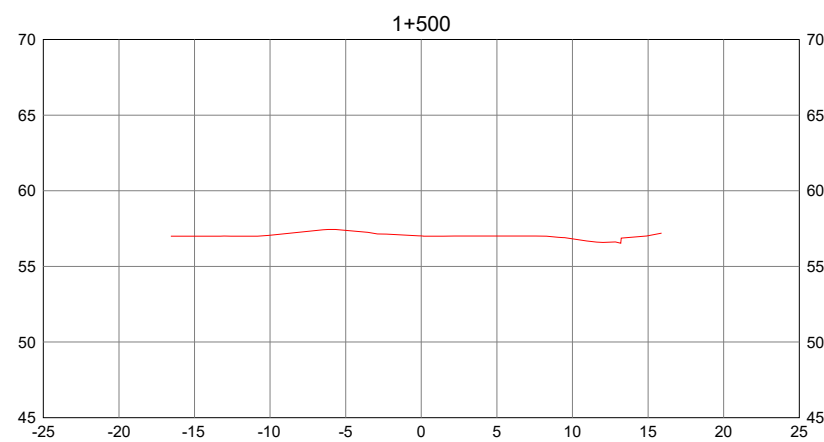

	:BUILDING		:DRAINAGE		:MAYOR CONTOUR
	:ROAD		:FENCE		:MINOR CONTOUR
	:BRIDGE		:CONTROL POINT (CP)		
	:RIVER		:BENCH MARK (BM)		

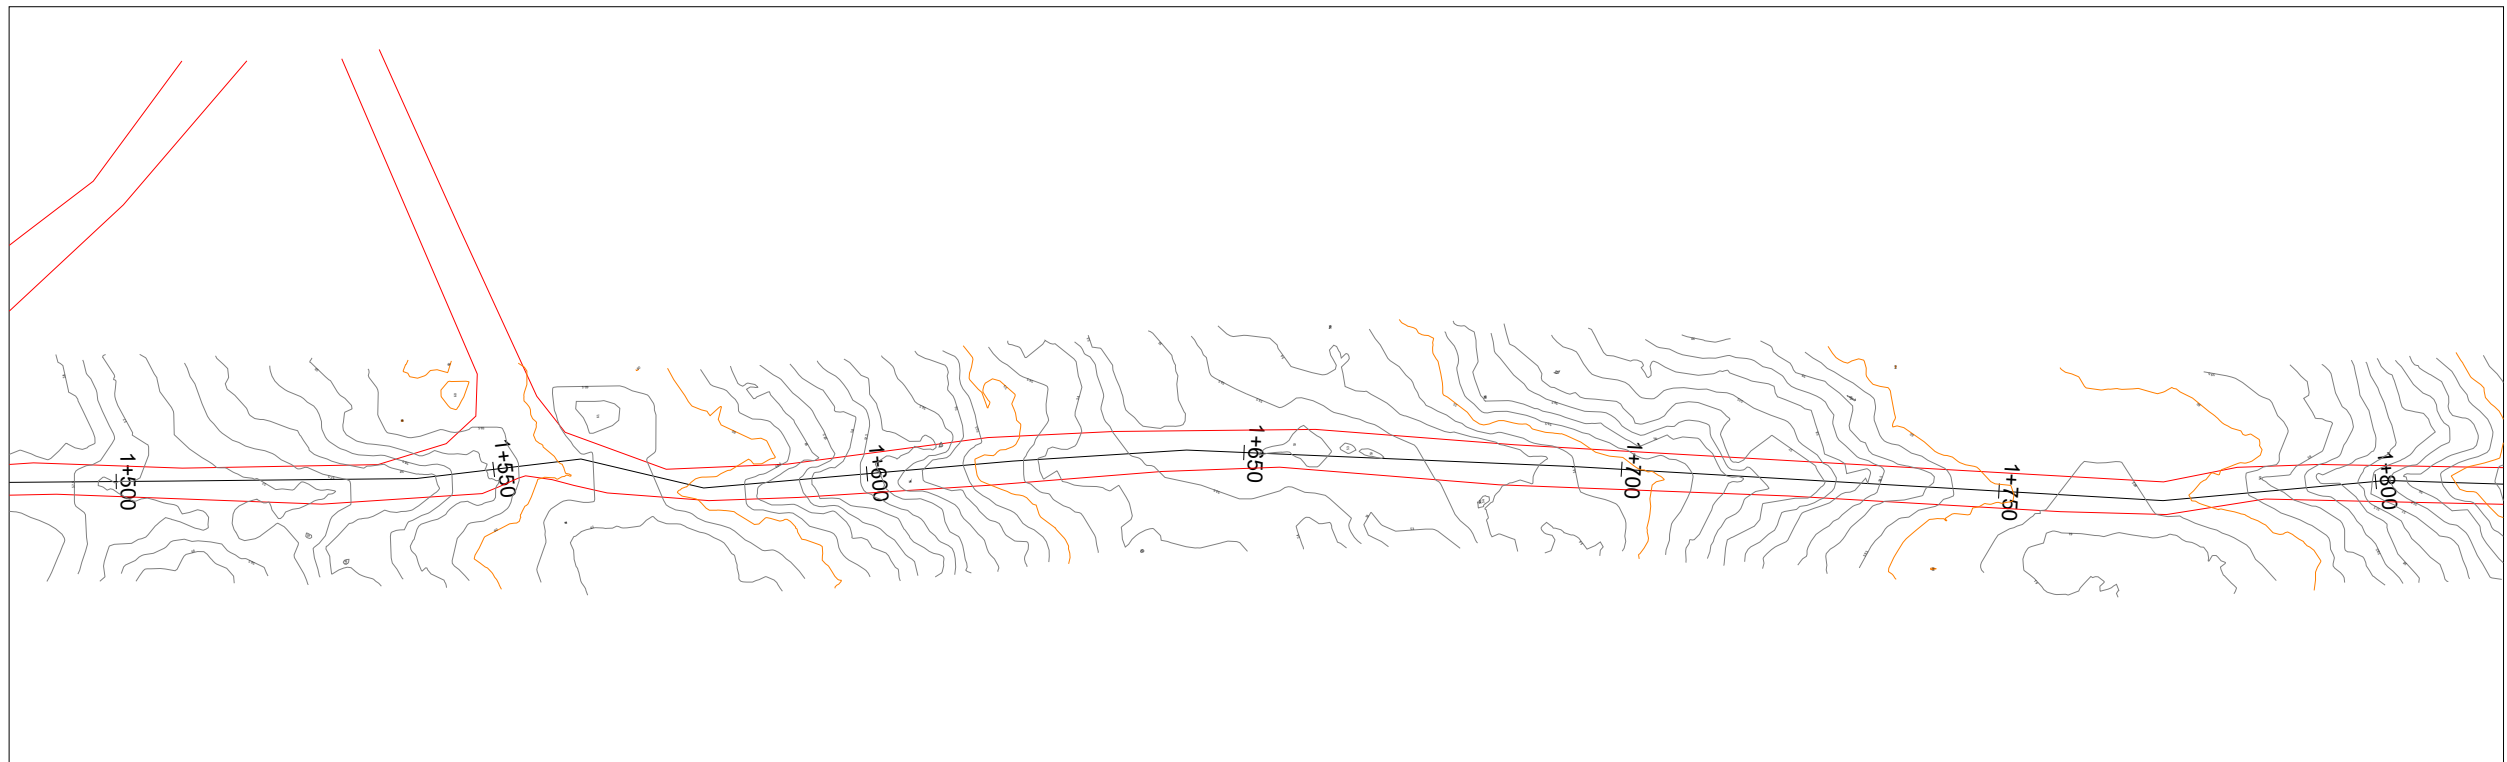

SCALE
1 : 1.000
1 : 200

REV.	5
------	---

0 |